# GROUND FLOOR PLAN

LEVEL +0.00 · 1:50 @ A1 · METRES

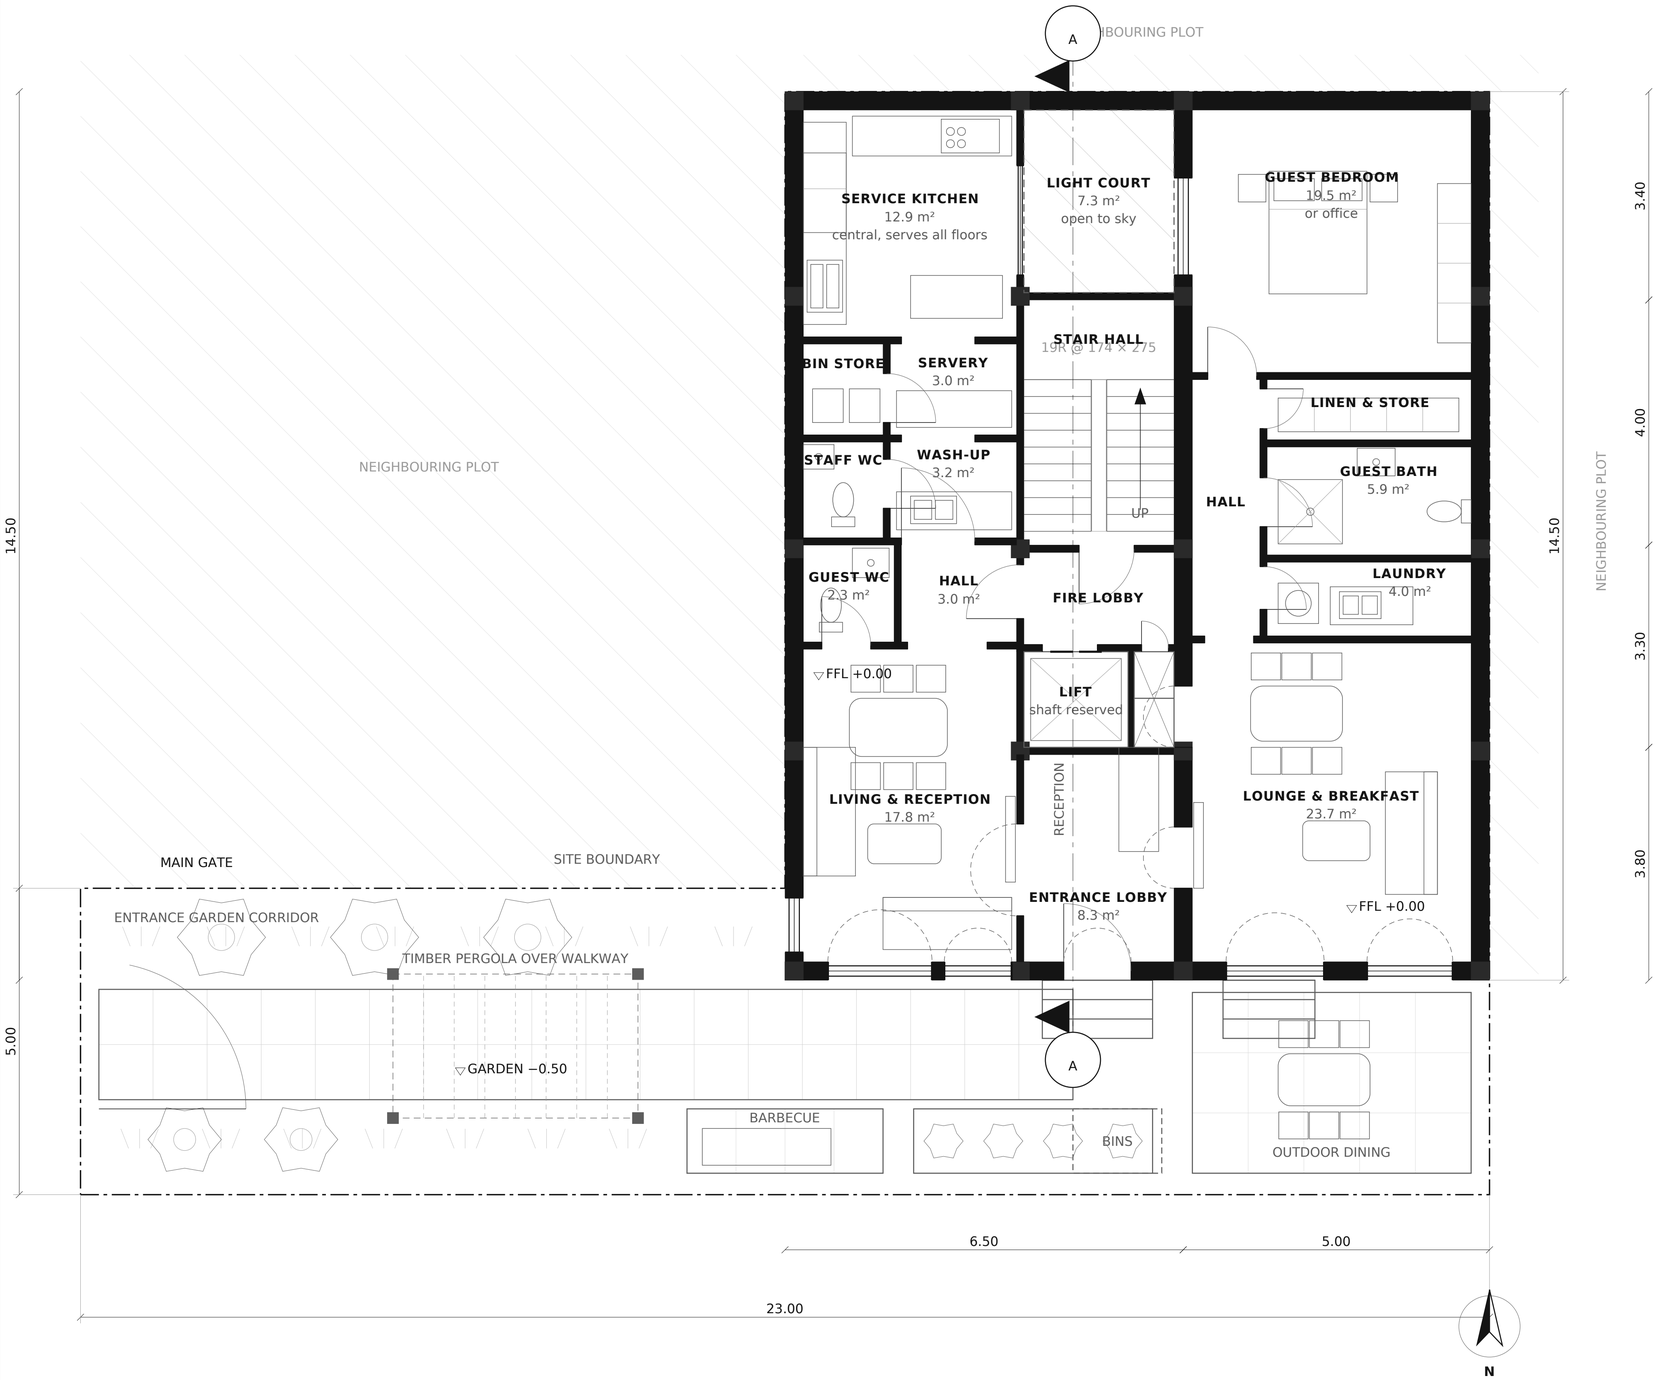


## KEY

- Masonry wall cut by section — 200 mm partition, 300 mm external / party
- Internal stud or block partition, 120 mm
- Terrace parapet, 250 mm × 1100 mm high
- Single leaf door, swing shown to opening side
- Glazed opening — arched head where noted
- Element above the cut plane (pergola, slab over)
- Void / open to sky
- ▽ +0.00 — Finished floor level datum

## AREA SCHEDULE

| | |
|---|---|
| ENTRANCE LOBBY & RECEPTION | 8.3 m² |
| LIVING & RECEPTION | 17.8 m² |
| GUEST WC | 2.3 m² |
| HALL | 3.0 m² |
| STAFF WC | 2.0 m² |
| WASH-UP | 3.2 m² |
| BIN STORE | 1.9 m² |
| SERVERY | 3.0 m² |
| SERVICE KITCHEN | 12.9 m² |
| LIFT SHAFT | 2.7 m² |
| FIRE LOBBY | 3.7 m² |
| PROTECTED STAIR | 9.8 m² |
| LOUNGE & BREAKFAST | 23.7 m² |
| HALL, BLOCK B | 4.6 m² |
| CENTRAL LAUNDRY | 4.0 m² |
| GUEST BATH | 5.9 m² |
| LINEN & STORE | 3.3 m² |
| GUEST BEDROOM | 19.5 m² |
| **TOTAL** | **131.5 m²** |
| GROSS INTERNAL AREA, THIS FLOOR | 140.0 m² |
| LIGHT COURT, OPEN TO SKY | 7.3 m² |
| SLAB TO SLAB | 3.30 m · 3.00 m clear |

## GENERAL NOTES

1. The whole of this floor is one non-residential compartment under the apartments: 2 hour separation to the floor over, sprinklered throughout, with a suppression hood over the cooking line.

2. The 12.9 m² service kitchen and the 4.0 m² laundry serve all four storeys, reached through the servery and the block B hall so that no room is entered through another. Kitchen extract rises in a fire-rated shaft in the riser cupboard off the fire lobby and discharges above roof level.

3. Living, reception, entrance lobby and the lounge read as one connected sequence through 1.00 m arched openings in the party wall. The guest WC opens off the reception and the guest bath off the block B hall, so neither is reached through the service route.

4. The east boundary wall is solid at this level: the adjoining owner may build up to 3.00 m against it. The kitchen and the guest bedroom are daylit from the light court, and the west wall is opened where it faces our own garden boundary — 3.00.

5. Bins are stored internally beside the kitchen. Guest bath, laundry, WCs and stores are internal, mechanically extracted at six air changes per hour. Gross internal area excludes the light court.

**FOUR STOREY VACATION HOME** — PRIVATE CLIENT

DRAWING

**GROUND FLOOR PLAN**

| DRAWING No | REVISION | SCALE | DATE |
|---|---|---|---|
| **A-100** | **P3** | **1:50 @ A1** | **2026-09-29** |

Preliminary design issue — not for construction.
Do not scale; work to figured dimensions only.

REVISIONS

P1 2026-09-18 first issue
P2 2026-09-24 east windows, taller floors, garden on A-100
P3 2026-09-29 four storeys, apartments, straight north boundary