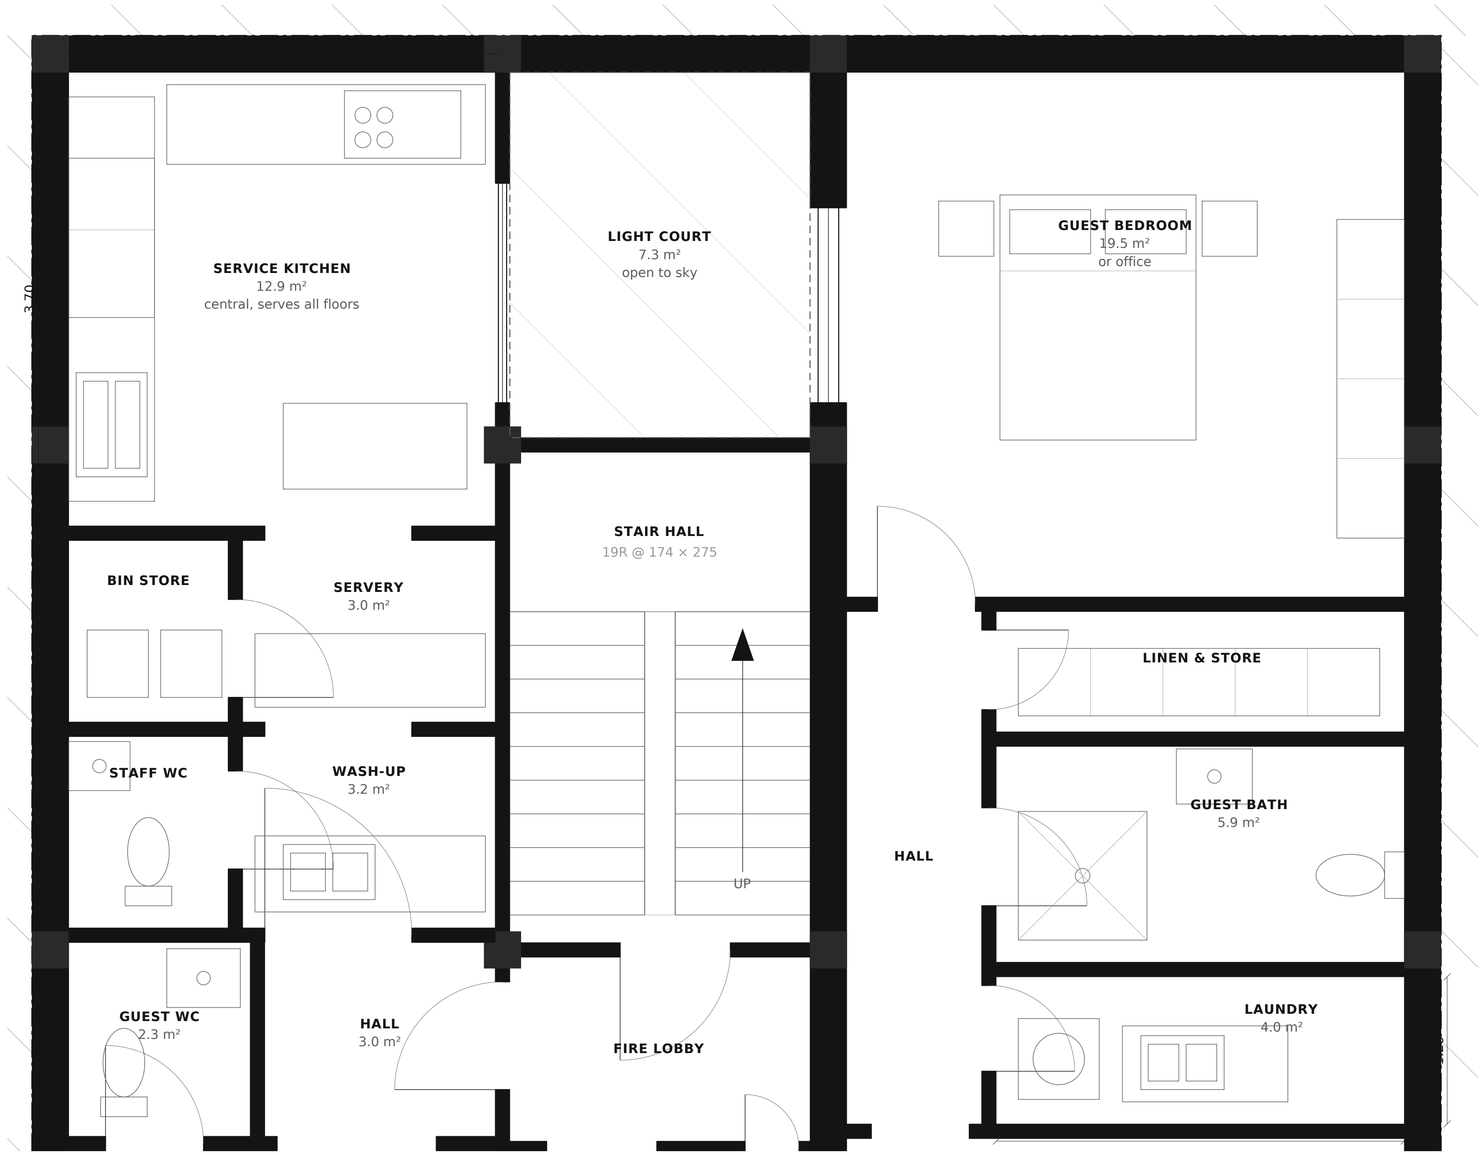

GRAPHIC SCALE 1:25

0 2 4 m

CENTRAL KITCHEN & LAUNDRY — ENLARGED PLAN

LEVEL +0.00 · 1:25 @ A1 · METRES

KEY

- Masonry wall cut by section — 200 mm partition, 300 mm external / party
- Internal stud or block partition, 120 mm
- Terrace parapet, 250 mm × 1100 mm high
- Single leaf door, swing shown to opening side
- Glazed opening — arched head where noted
- Element above the cut plane (pergola, slab over)
- Void / open to sky
- ▽ +0.00 Finished floor level datum

AREA SCHEDULE

SERVICE KITCHEN	12.9 m²
SERVERY	3.0 m²
WASH-UP	3.2 m²
STAFF WC	2.0 m²
BIN STORE	1.9 m²
CENTRAL LAUNDRY	4.0 m²
GUEST BATH	5.9 m²
LINEN & STORE	3.3 m²
TOTAL	**36.2 m²**
KITCHEN, PREVIOUS ISSUE	18.4 m²
KITCHEN, THIS ISSUE	12.9 m² (−30 %)
LAUNDRY, PREVIOUS ISSUE	10.4 m²
LAUNDRY, THIS ISSUE	4.0 m²

GENERAL NOTES

1. Enlarged from A-100. The kitchen is reduced 30 % on the client's instruction; the area released carries a staff WC, an internal bin store and a servery on the route in, so bins no longer stand out on the patio.

2. Kitchen fit-out: a wet run on the west wall with a deep bowl sink and undercounter refrigeration, a cooking line on the north wall under the extract hood, and a free-standing preparation counter between them.

3. Laundry takes one washer-dryer, a utility sink and a folding counter, as instructed. Linen and housekeeping stores are next to it off the same hall.

4. The hall in block B is 1.10 m clear and serves the laundry, the guest bath, the linen store and the guest bedroom, so none of them is entered through another room.

5. Kitchen extract rises in a fire-rated shaft inside the riser cupboard off the fire lobby and discharges above roof level. Suppression over the cooking line; 2 hour separation to the floor over.

FOUR-STOREY VACATION HOME — PRIVATE CLIENT

DRAWING

CENTRAL KITCHEN & LAUNDRY — ENLARGED PLAN

DRAWING No	REVISION	SCALE	DATE
A-302	**P3**	**1:25 @ A1**	**2026-09-29**

Preliminary design issue — not for construction.
Do not scale; work to figured dimensions only.

REVISIONS
P1 2026-09-18 first issue
P2 2026-09-24 east windows, taller floors, garden on A-100
P3 2026-09-29 four storeys, apartments, straight north boundary