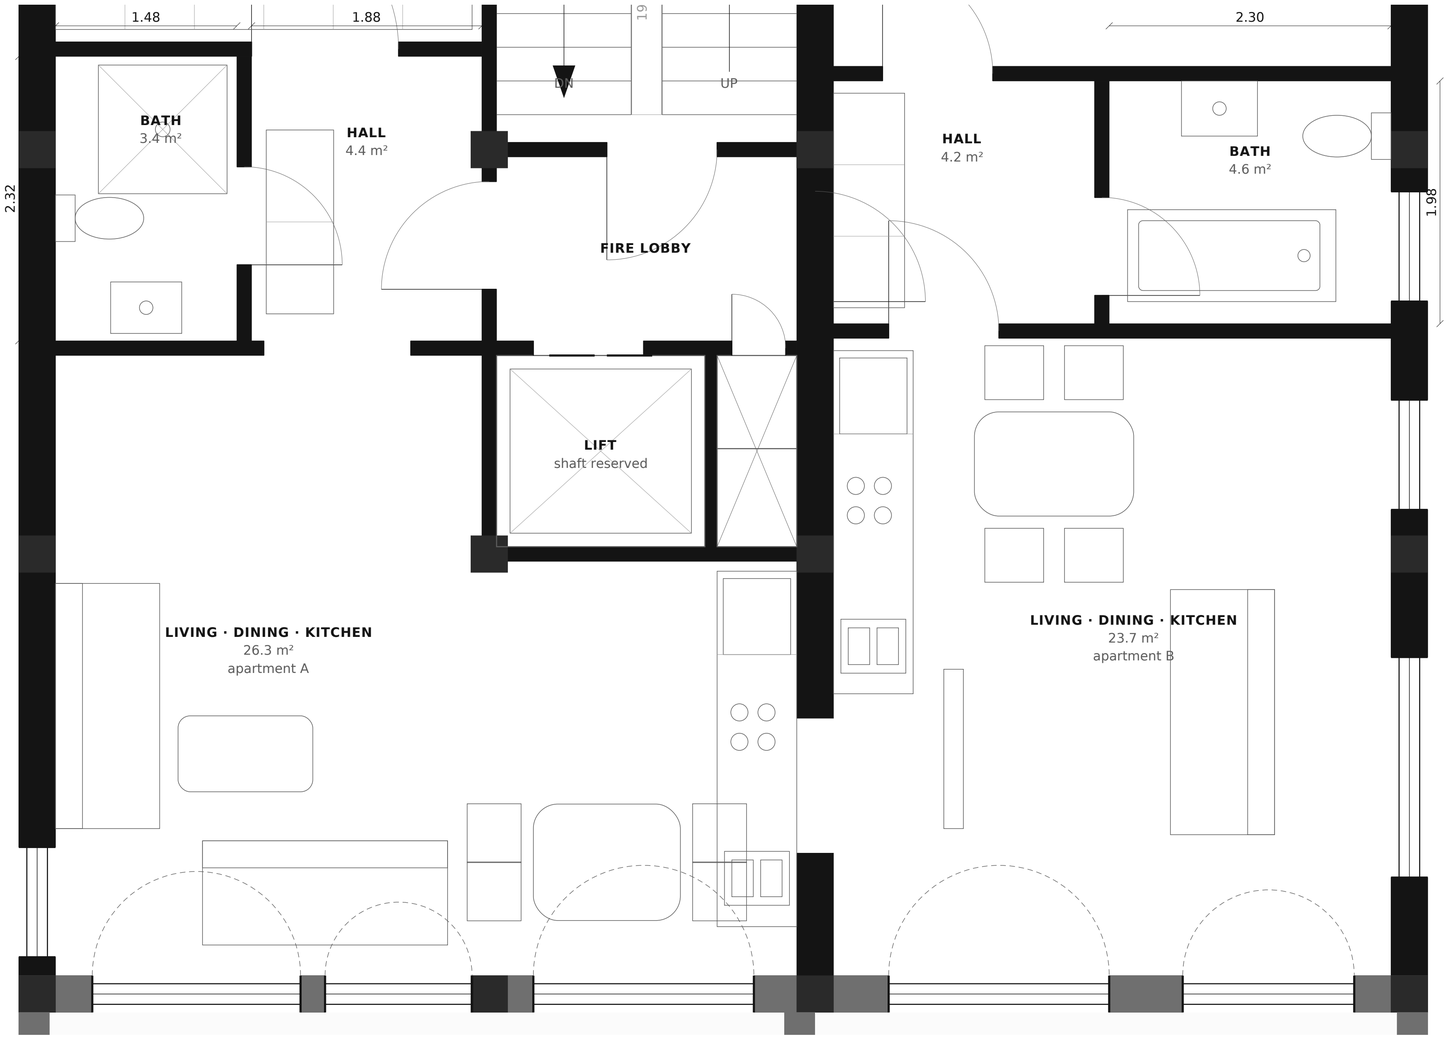

GRAPHIC SCALE 1:25

0 2 4 m

TYPICAL APARTMENT — ENLARGED PLAN

LEVEL +3.30 / +6.60 · 1:25 @ A1 · METRES

KEY

- Masonry wall cut by section — 200 mm partition, 300 mm external / party
- Internal stud or block partition, 120 mm
- Terrace parapet, 250 mm × 1100 mm high
- Single leaf door, swing shown to opening side
- Glazed opening — arched head where noted
- Element above the cut plane (pergola, slab over)
- Void / open to sky
- +0.00 Finished floor level datum

AREA SCHEDULE

APT A BATHROOM	3.4 m²
APT A ENTRY HALL	4.4 m²
APT A LIVING / KITCHEN	26.3 m²
APT B ENTRY HALL	4.2 m²
APT B BATHROOM	4.6 m²
APT B LIVING / KITCHEN	23.7 m²
TOTAL	**66.6 m²**
APARTMENT A / APARTMENT B	64.7 / 63.2 m²
BALCONY A / B (EXTERNAL)	7.8 / 6.0 m²

GENERAL NOTES

1. Enlarged from A-101; the second floor is identical. Only the entry, wet rooms and kitchenettes are shown at this scale — a whole 13.90 m unit does not fit an A1 sheet at 1:25.

2. Apartment A: bathroom and entry hall side by side on the front door, so the bathroom is reached from the hall and from the bedroom without crossing the living room. Kitchenette runs against the party wall in the south-east bay.

3. Apartment B: bathroom off its own entry hall with a window in the open east wall, kitchenette against the party wall opposite apartment A's riser.

4. All kitchenettes are one joinery run: 600 mm sink bay, two-ring induction hob, undercounter fridge and overhead storage over the full length. Recirculating hood unless a duct to the riser is confirmed.

5. Every wet room drains to the riser cupboard on the party wall; runs longer than 2 m fall at 1:40 within the 300 mm floor zone.

FIVE-STOREY VACATION VILLA — PRIVATE CLIENT

DRAWING

TYPICAL APARTMENT — ENLARGED PLAN

DRAWING No	REVISION	SCALE	DATE
A-300	**P4**	**1:25 @ A1**	**2026-10-07**

Preliminary design issue — not for construction.
Do not scale; work to figured dimensions only.

REVISIONS
P1 2026-09-18 first issue
P2 2026-09-24 east windows, taller floors, garden on A-100
P3 2026-09-29 four storeys, apartments, straight north boundary
P4 2026-09-29 north and east opened up, light court removed