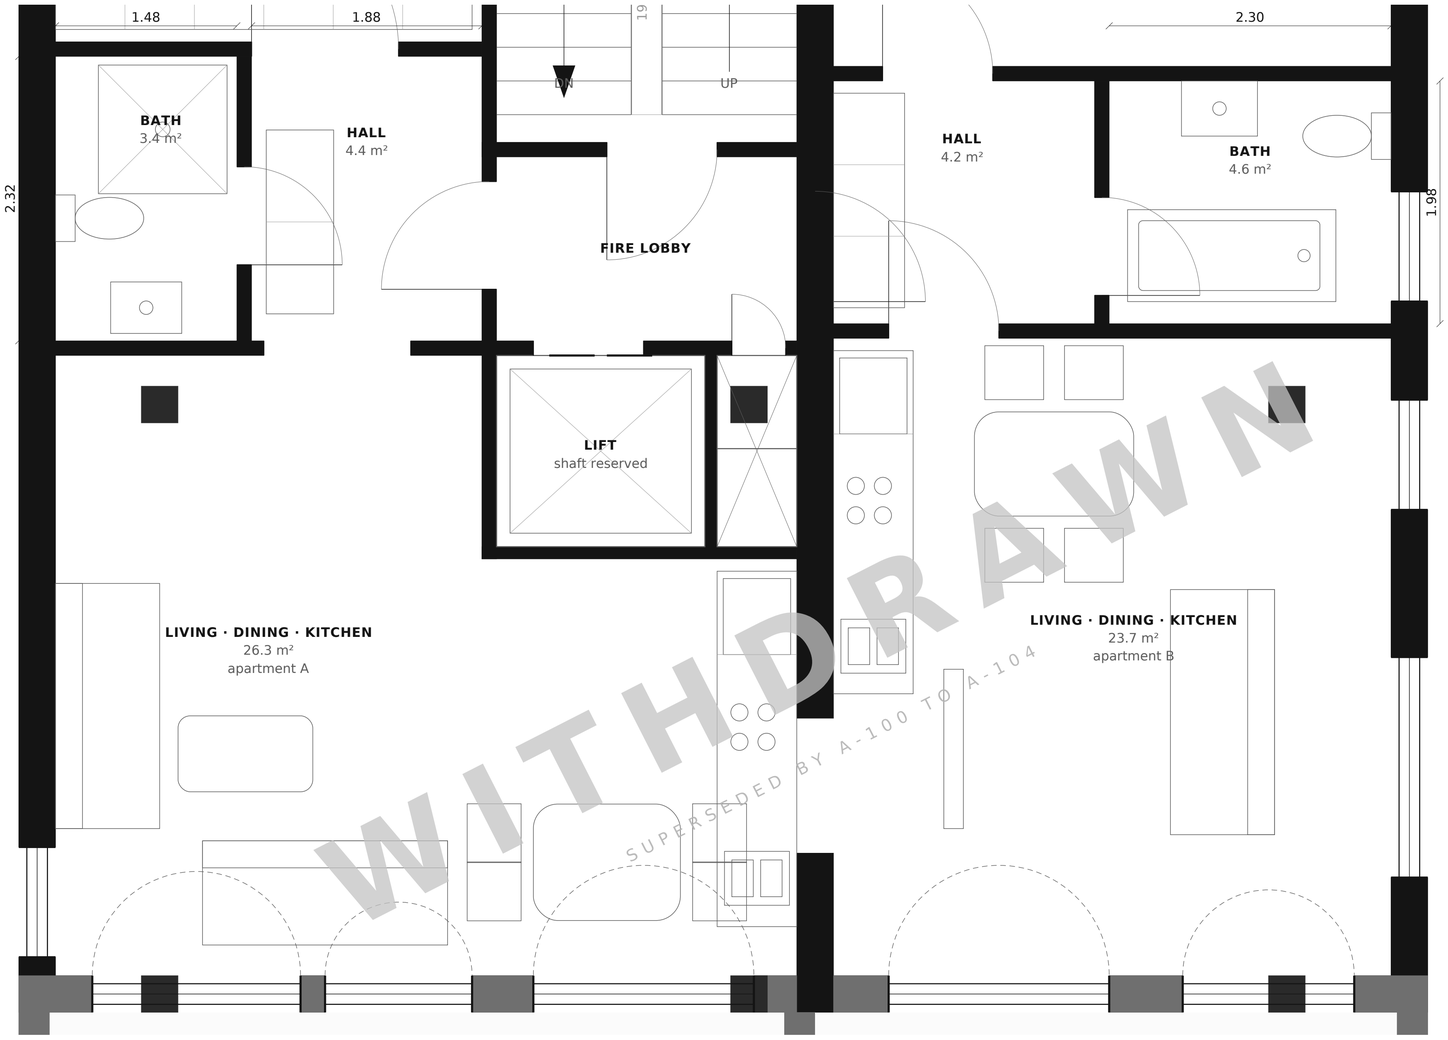

WITHDRAWN
SUPERSEDED BY A-100 TO A-104

GRAPHIC SCALE 1:25

0 2 4 m

TYPICAL APARTMENT — ENLARGED PLAN

LEVEL +3.30 / +6.60 · 1:25 @ A1 · METRES

KEY

- External / party wall cut by section, 300 mm — brick, colour unrestricted
- Internal partition, 100 mm — red brick
- Terrace parapet, 250 mm × 1100 mm high
- Single leaf door, swing shown to opening side
- Glazed opening — arched head where noted
- Element above the cut plane (pergola, slab over)
- Void / open to sky
- +0.00 Finished floor level datum

AREA SCHEDULE

APT A BATHROOM	3.4 m²
APT A ENTRY HALL	4.4 m²
APT A LIVING / KITCHEN	26.3 m²
APT B ENTRY HALL	4.2 m²
APT B BATHROOM	4.6 m²
APT B LIVING / KITCHEN	23.7 m²
TOTAL	**66.6 m²**
APARTMENT A / APARTMENT B	64.7 / 63.2 m²
BALCONY A / B (EXTERNAL)	7.8 / 6.0 m²

GENERAL NOTES

1. Enlarged from A-101; the second floor is identical. Only the entry, wet rooms and kitchenettes are shown at this scale — a whole 13.90 m unit does not fit an A1 sheet at 1:25.

2. Apartment A: bathroom and entry hall side by side on the front door, so the bathroom is reached from the hall and from the bedroom without crossing the living room. Kitchenette runs against the party wall in the south-east bay.

3. Apartment B: bathroom off its own entry hall with a window in the open east wall, kitchenette against the party wall opposite apartment A's riser.

4. All kitchenettes are one joinery run: 600 mm sink bay, two-ring induction hob, undercounter fridge and overhead storage over the full length. Recirculating hood unless a duct to the riser is confirmed.

5. Every wet room drains to the riser cupboard on the party wall; runs longer than 2 m fall at 1:40 within the 300 mm floor zone.

FIVE-STOREY VACATION VILLA — SHAMANDEEL, QUESNA, MENOUFIA, EGYPT

DRAWING

TYPICAL APARTMENT — ENLARGED PLAN

DRAWING No	REVISION	SCALE	DATE
A-300	**P22**	**1:25 @ A1**	**2026-10-10**

Withdrawn at P22 — superseded by A-100 to A-104. Record only; not for construction, pricing or measurement. Do not scale; work to figured dimensions only.

REVISIONS

P19 2026-10-07 serpentine waist deepened 0.75 to 1.35 m; 15.7 m² of balcony a floor
P20 2026-10-07 internal partitions 100 mm red brick, specified by the client
P21 2026-10-07 300 mm external and party walls: brick, colour unrestricted
P22 2026-10-08 A-300 to A-302 withdrawn: enlargements of a building not being built