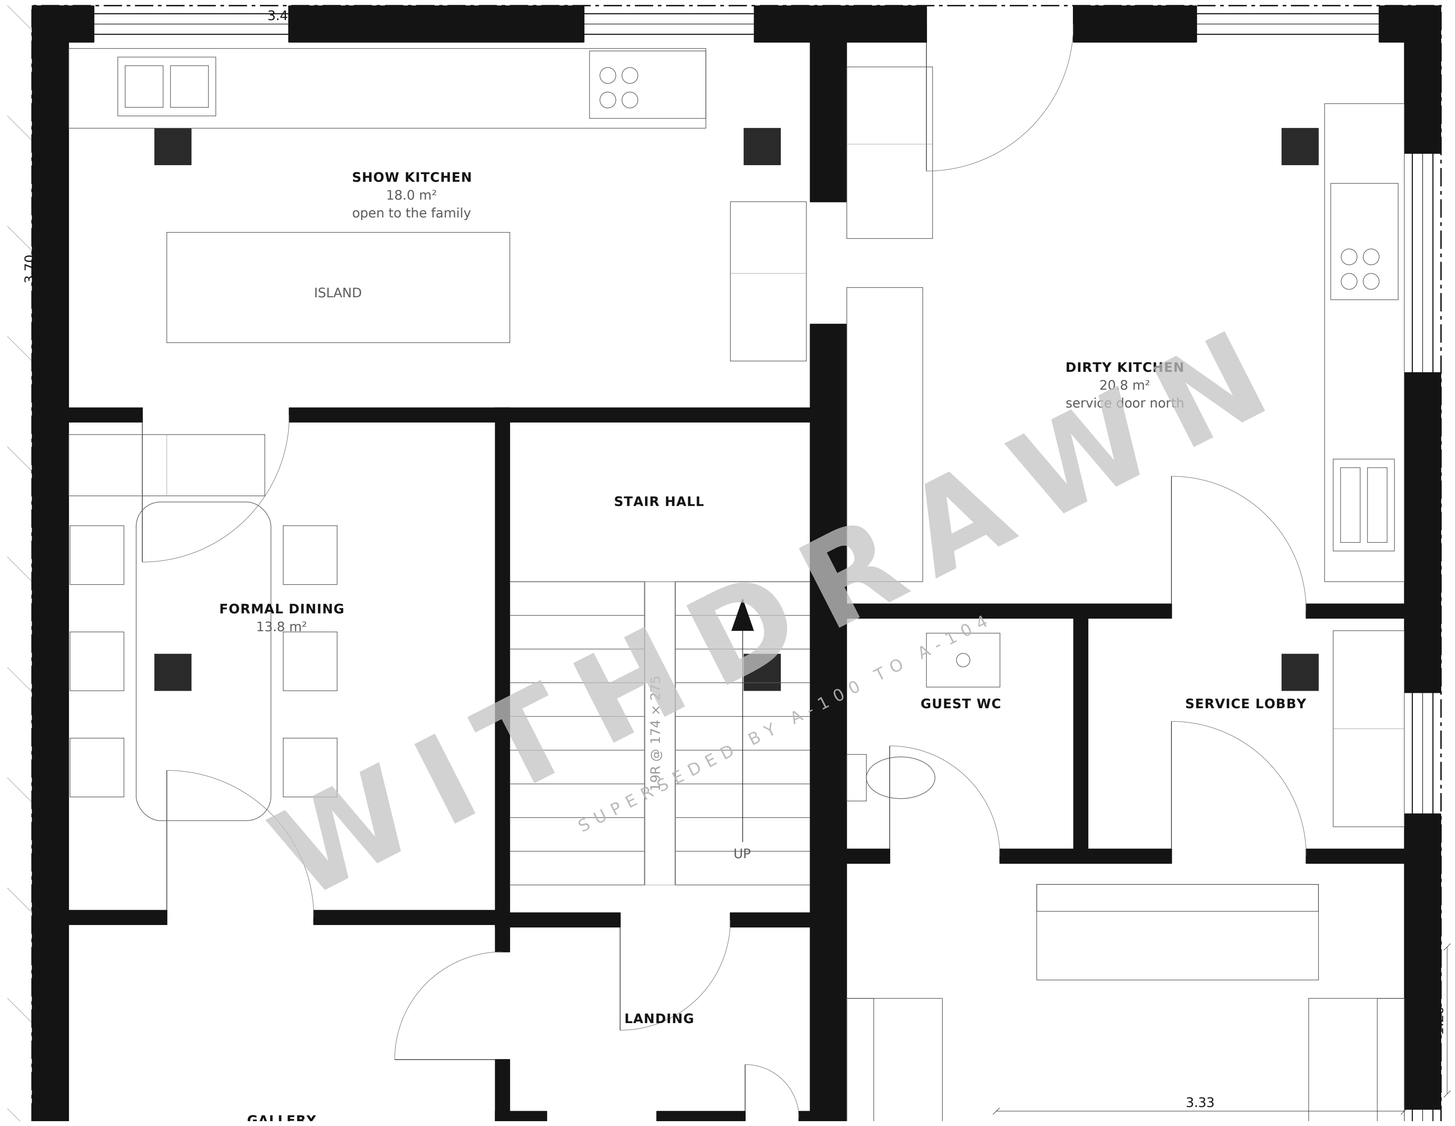

GRAPHIC SCALE 1:25

0 2 4 m

CENTRAL KITCHEN & LAUNDRY — ENLARGED PLAN

LEVEL +0.00 · 1:25 @ A1 · METRES

KEY

- External / party wall cut by section, 300 mm — brick, colour unrestricted
- Internal partition, 100 mm — red brick
- Terrace parapet, 250 mm × 1100 mm high
- Single leaf door, swing shown to opening side
- Glazed opening — arched head where noted
- Element above the cut plane (pergola, slab over)
- Void / open to sky
- +0.00 — Finished floor level datum

AREA SCHEDULE

SERVICE KITCHEN	12.9 m²
SERVERY	3.0 m²
WASH-UP	3.2 m²
STAFF WC	2.0 m²
BIN STORE	1.9 m²
CENTRAL LAUNDRY	4.0 m²
GUEST BATH	5.9 m²
LINEN & STORE	3.3 m²
TOTAL	**36.2 m²**
KITCHEN, PREVIOUS ISSUE	18.4 m²
KITCHEN, THIS ISSUE	12.9 m² (−30 %)
LAUNDRY, PREVIOUS ISSUE	10.4 m²
LAUNDRY, THIS ISSUE	4.0 m²

GENERAL NOTES

1. Enlarged from A-100. The kitchen is reduced 30 % on the client's instruction; the area released carries a staff WC, an internal bin store and a servery on the route in, so bins no longer stand out on the patio.

2. Kitchen fit-out: a wet run on the west wall with a deep bowl sink and undercounter refrigeration, a cooking line on the north wall under the extract hood, and a free-standing preparation counter between them.

3. Laundry takes one washer-dryer, a utility sink and a folding counter, as instructed. Linen and housekeeping stores are next to it off the same hall.

4. The hall in block B is 1.10 m clear and serves the laundry, the guest bath, the linen store and the guest bedroom, so none of them is entered through another room.

5. Kitchen extract rises in a fire-rated shaft inside the riser cupboard off the fire lobby and discharges above roof level. Suppression over the cooking line; 2 hour separation to the floor over.

FIVE-STOREY VACATION VILLA — SHAMANDEEL, QUESNA, MENOUFIA, EGYPT

DRAWING

CENTRAL KITCHEN & LAUNDRY — ENLARGED PLAN

DRAWING No	REVISION	SCALE	DATE
A-302	**P22**	**1:25 @ A1**	**2026-10-10**

Withdrawn at P22 — superseded by A-100 to A-104. Record only; not for construction, pricing or measurement. Do not scale; work to figured dimensions only.

REVISIONS

P19 2026-10-07 serpentine waist deepened 0.75 to 1.35 m; 15.7 m² of balcony a floor
P20 2026-10-07 internal partitions 100 mm red brick, specified by the client
P21 2026-10-07 300 mm external and party walls: brick, colour unrestricted
P22 2026-10-08 A-300 to A-302 withdrawn: enlargements of a building not being built