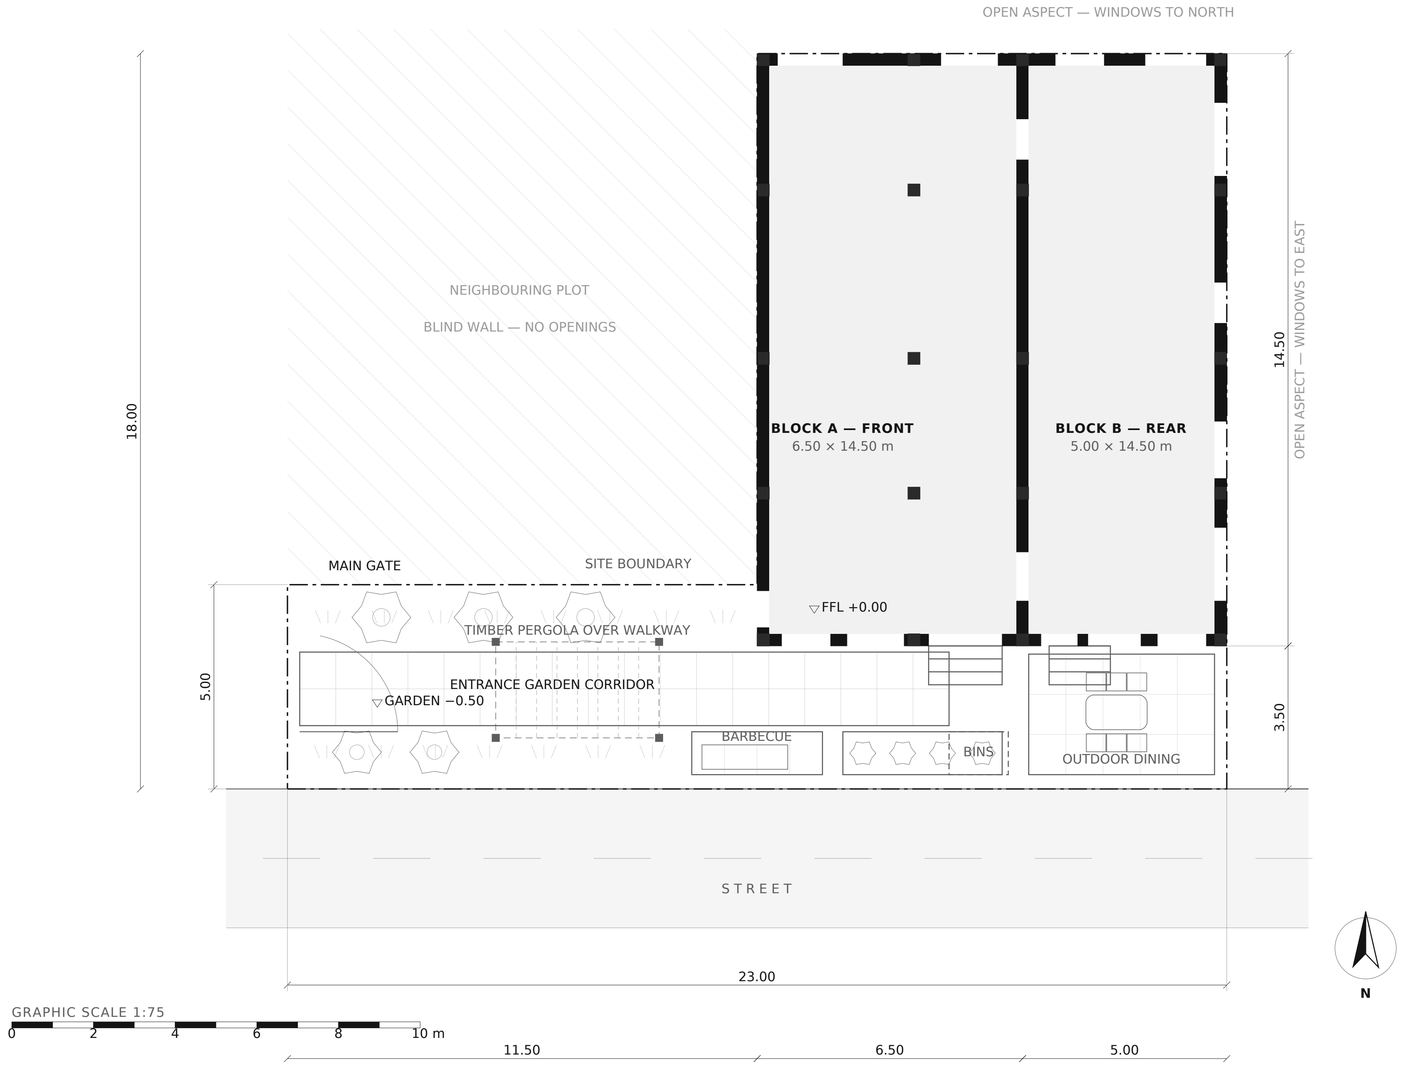

SITE PLAN

LEVEL +0.00 · 1:75 @ A1 · METRES

KEY

- Masonry wall cut by section — 200 mm partition, 300 mm external / party
- Internal stud or block partition, 120 mm
- Terrace parapet, 250 mm × 1100 mm high
- Single leaf door, swing shown to opening side
- Glazed opening — arched head where noted
- Element above the cut plane (pergola, slab over)
- Void / open to sky
- ▽ +0.00 — Finished floor level datum

AREA SCHEDULE

GARDEN CORRIDOR, WEST 11.50 × 5.00	57.5 m²
GARDEN CORRIDOR, FRONT 11.50 × 3.50	40.2 m²
BLOCK A FOOTPRINT 6.50 × 14.50	94.2 m²
BLOCK B FOOTPRINT 5.00 × 14.50	72.5 m²
TOTAL	**264.5 m²**
BUILT FOOTPRINT	166.8 m²
SITE COVERAGE	63.0 %
GROSS INTERNAL AREA, FOUR STOREYS	577.1 m²

GENERAL NOTES

1. The client's survey sketch recorded a 0.50 m step in the north boundary and a 5.50 m offset between the two blocks' north walls; the two cannot both be true. Resolved in favour of a straight boundary at 18.00, with both blocks running north to meet it. To be confirmed by measured survey before any work starts on site.

2. The south wall of both blocks stands 1.50 m further into the garden than the previous issue, giving each block a 14.50 m depth. The garden corridor is 5.00 m deep west of the building and 3.50 m deep in front of it.

3. Upper floor balconies cantilever a further 1.20 m south of that wall. Nothing projects over a boundary, but the overhang is subject to the local projection rule; confirm before construction.

4. Only the west boundary is built against, so the west wall is blind except where it faces the plot's own garden. The north and east boundaries are open on the client's confirmation and are windowed on every floor; the light court shown in P3 has gone.

5. The ground floor sits 0.50 m above the garden, reached by three risers at 167 mm at the entrance and at the patio doors.

6. Structure is an RC frame on the grid shown, columns set out on wall centrelines so none stands in a room; flat slab where spans and layout make it the simpler solution.

FOUR-STOREY VACATION HOME — PRIVATE CLIENT

DRAWING

SITE PLAN

DRAWING No	REVISION	SCALE	DATE
A-000	**P4**	**1:75 @ A1**	**2026-10-07**

Preliminary design issue — not for construction.
Do not scale; work to figured dimensions only.

REVISIONS
P1 2026-09-18 first issue
P2 2026-09-24 east windows, taller floors, garden on A-100
P3 2026-09-29 four storeys, apartments, straight north boundary
P4 2026-09-29 north and east opened up, light court removed