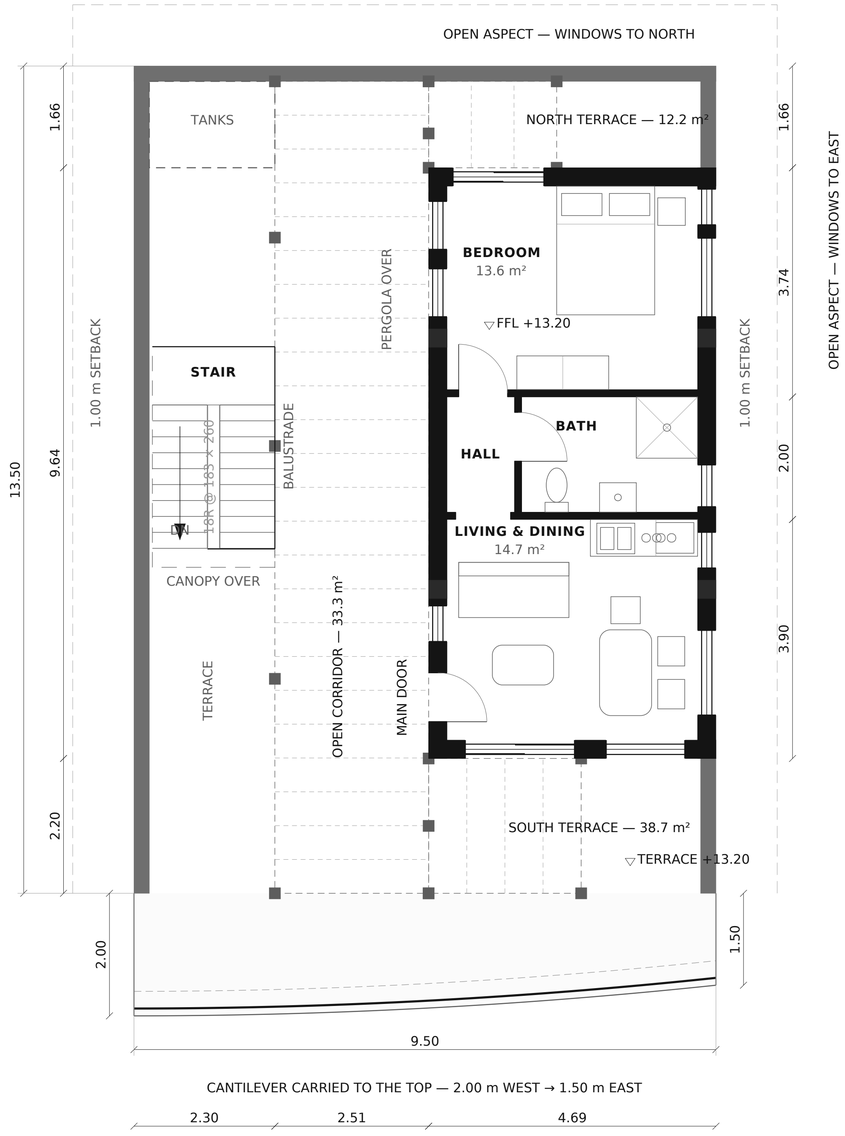


GRAPHIC SCALE 1:50

0 2 4 6 8 10 m

N

# PENTHOUSE PLAN — DETACHED VILLA

LEVEL +13.20 · 1:50 @ A1 · METRES

## KEY

- Masonry wall cut by section — 200 mm partition, 300 mm external / party
- Internal stud or block partition, 120 mm
- Terrace parapet, 250 mm × 1100 mm high
- Single leaf door, swing shown to opening side
- Glazed opening — arched head where noted
- Element above the cut plane (pergola, slab over)
- Void / open to sky
- ▽ +0.00 — Finished floor level datum

## AREA SCHEDULE

| | |
|---|---|
| LIVING AND DINING | 14.7 m² |
| HALL | 2.1 m² |
| BATH | 5.4 m² |
| BEDROOM | 13.6 m² |
| **TOTAL** | **35.8 m²** |
| GROSS INTERNAL AREA, FLAT | 37.0 m² |
| SOUTH TERRACE | 38.7 m² |
| NORTH TERRACE | 12.2 m² |
| OPEN CORRIDOR | 33.3 m² |
| TOP OF PENTHOUSE SLAB | +16.45 |
| FLOOR BELOW | +9.90 |

## GENERAL NOTES

1. Draft for comment. The two open areas are joined outside the flat, down the west side, by a corridor 2.51 m clear against the 2.00 m asked for, with the pergola running over its whole length.

2. 37.0 m² indoors; 38.7 m² of terrace south, 12.2 m² north and 33.3 m² of corridor between them. The front door is off the corridor.

3. The corridor passes east of the stair, not west: the well is 2.00 m wide and hard against the west parapet, and its half landing is 1.65 m below this floor, so it stays open.

4. Its east side is the flat's west wall, which stands on the spine at x 17.46 - the one line on this side of the roof with a beam under it. That leaves the flat 4.09 m clear, which will not take two bedrooms side by side: stacking them needs 12.06 m of the 13.50 m depth and leaves 1.44 m for both terraces. The second bedroom is what pays for the corridor.

5. Both long walls swallow a column line - x 17.46 and x 21.85, with the columns at y 8.46 and 12.56 inside the wall. The short walls sit on secondary beams cast in the roof slab, spanning the 4.39 m between those lines.

6. At +16.45 the penthouse is a fourth storey for most planning codes. The site plan, section A—A and the A-300 enlargements are still on the old 11.50 × 14.50 footprint.

**FOUR-STOREY VACATION HOME** — PRIVATE CLIENT

DRAWING

**PENTHOUSE PLAN — DETACHED VILLA**

| DRAWING No | REVISION | SCALE | DATE |
|---|---|---|---|
| **A-104** | **P11** | **1:50 @ A1** | **2026-10-07** |

Preliminary design issue — not for construction.
Do not scale; work to figured dimensions only.

REVISIONS

P8 2026-10-06 ground floor opened up; guest room off the hall
P9 2026-10-06 penthouse added: two-bedroom roof apartment
P10 2026-10-07 penthouse between two terraces, pergola joining them
P11 2026-10-07 penthouse: 2.51 m corridor outside the flat, west side