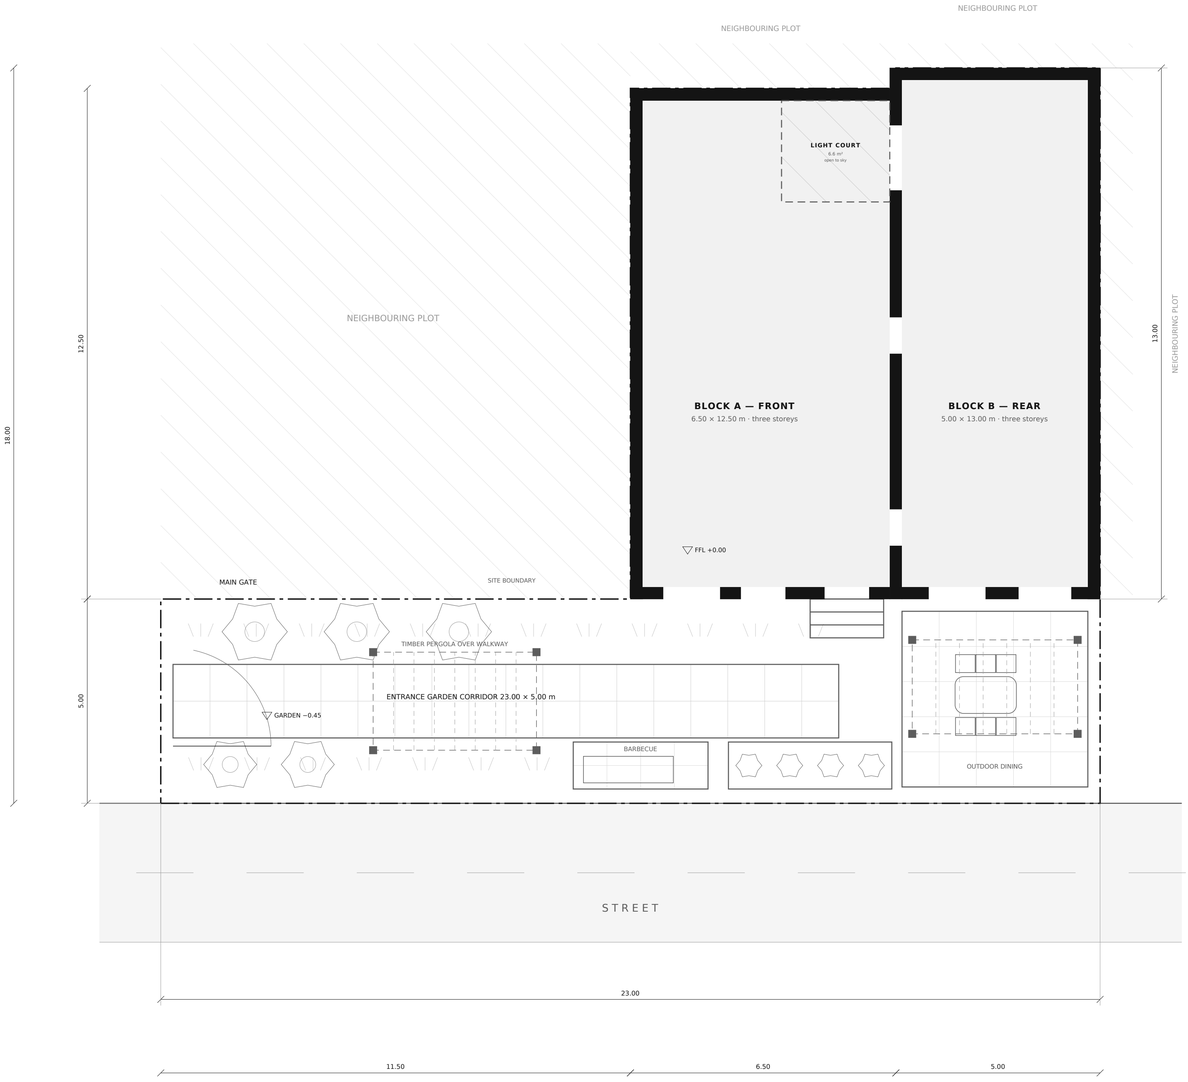

GRAPHIC SCALE 1:75

0 2 4 6 8 10 m

N

SITE PLAN

LEVEL +0.00 · SCALE 1:75 @ A1 · ALL DIMENSIONS IN METRES

KEY

- Masonry wall cut by section — 200 mm partition, 300 mm external / party
- Internal stud or block partition, 120 mm
- Terrace parapet, 250 mm × 1100 mm high
- Single leaf door, swing shown to opening side
- Glazed opening — arched head where noted
- Element above the cut plane (pergola, slab over)
- Void / open to sky
- +0.00 — Finished floor level datum

AREA SCHEDULE

GARDEN CORRIDOR 23.00 × 5.00	115.0 m²
BLOCK A FOOTPRINT 6.50 × 12.50	81.2 m²
BLOCK B FOOTPRINT 5.00 × 13.00	65.0 m²
TOTAL	**261.2 m²**
BUILT FOOTPRINT	146.3 m²
SITE COVERAGE	56.0 %
GROSS INTERNAL AREA, THREE STOREYS	258.0 m²

GENERAL NOTES

1. Site boundaries and the 23.00 × 5.00 m garden corridor are taken from the client's survey sketch. All boundary dimensions to be confirmed by measured survey before any work starts on site.

2. Blocks A and B sit hard against the north, east and west boundaries. The south elevation onto the garden is the only open facade, so a 2.65 × 2.48 m light court is cut through all three storeys to daylight the centre of the plan.

3. The garden falls 0.45 m from the house threshold to the gate. Surface water to a soakaway within the planted border.

4. No part of the new work oversails or undermines the adjoining plots; party wall notices to be served on the north, east and west owners before excavation.

VACATION HOUSE — NEW BUILD

PRIVATE CLIENT

DRAWING

SITE PLAN

DRAWING No	REVISION	SCALE	DATE
A-000	**P1**	**1:75 @ A1**	**2026-09-18**

Preliminary design issue — not for construction. Do not scale from this drawing; work to figured dimensions only and verify all levels and site boundaries before work.