SECOND FLOOR & ROOF PLAN

LEVEL +6.00 · SCALE 1:50 @ A1 · ALL DIMENSIONS IN METRES

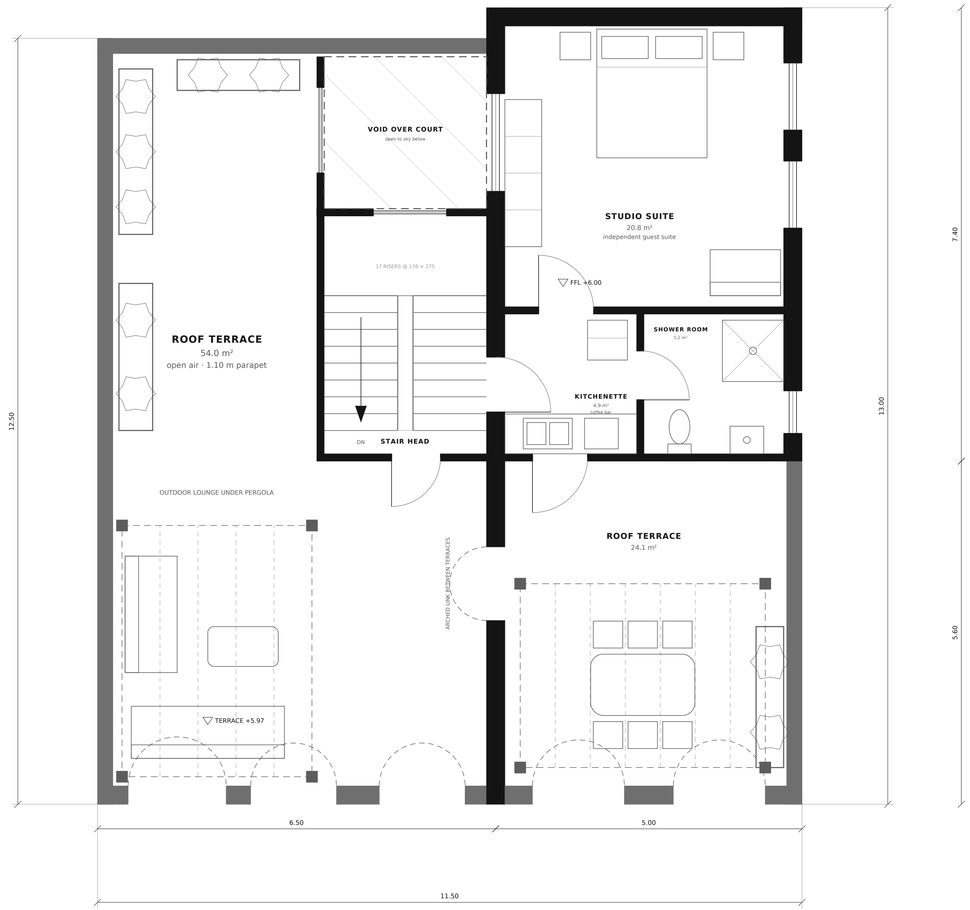

KEY

- Masonry wall cut by section — 200 mm partition, 300 mm external / party
- Internal stud or block partition, 120 mm
- Terrace parapet, 250 mm × 1100 mm high
- Single leaf door, swing shown to opening side
- Glazed opening — arched head where noted
- Element above the cut plane (pergola, slab over)
- Void / open to sky
- +0.00 — Finished floor level datum

AREA SCHEDULE

ROOF TERRACE	54.0 m²
STAIR HEAD	10.6 m²
ROOF TERRACE, BLOCK B	24.1 m²
KITCHENETTE	4.9 m²
SHOWER ROOM	5.2 m²
STUDIO SUITE	20.8 m²
TOTAL	**119.6 m²**
GROSS INTERNAL AREA, THIS FLOOR	41.5 m²
OPEN-AIR TERRACE, BOTH BLOCKS	78.1 m²

GENERAL NOTES

1. Block A is given over entirely to an open-air roof terrace at this level, apart from the stair head and the light court void.
2. Timber pergolas are set out on a 550 mm rafter pitch over the lounge and the outdoor table; both are shown dashed as they sit above the cut plane.
3. The studio suite is self-contained, with its own shower room and kitchenette, and is entered from the stair head without crossing the family floor below.
4. The studio cross ventilates between the light court on the west and two east windows; the shower room has an openable east window in place of mechanical extract. East boundary openings are subject to local fire separation and rights of light rules; confirm before construction.
5. Roof falls 1:60 to rainwater outlets at the parapet; waterproofing turned up 150 mm minimum behind the terrace finish.

GRAPHIC SCALE 1:50

0 — 2 — 4 — 6 — 8 — 10 m

N

VACATION HOUSE — NEW BUILD

PRIVATE CLIENT

DRAWING

SECOND FLOOR & ROOF PLAN

DRAWING No	REVISION	SCALE	DATE
A-102	P1	1:50 @ A1	2026-09-18

Preliminary design issue — not for construction. Do not scale from this drawing; work to figured dimensions only and verify all levels and site boundaries before work.