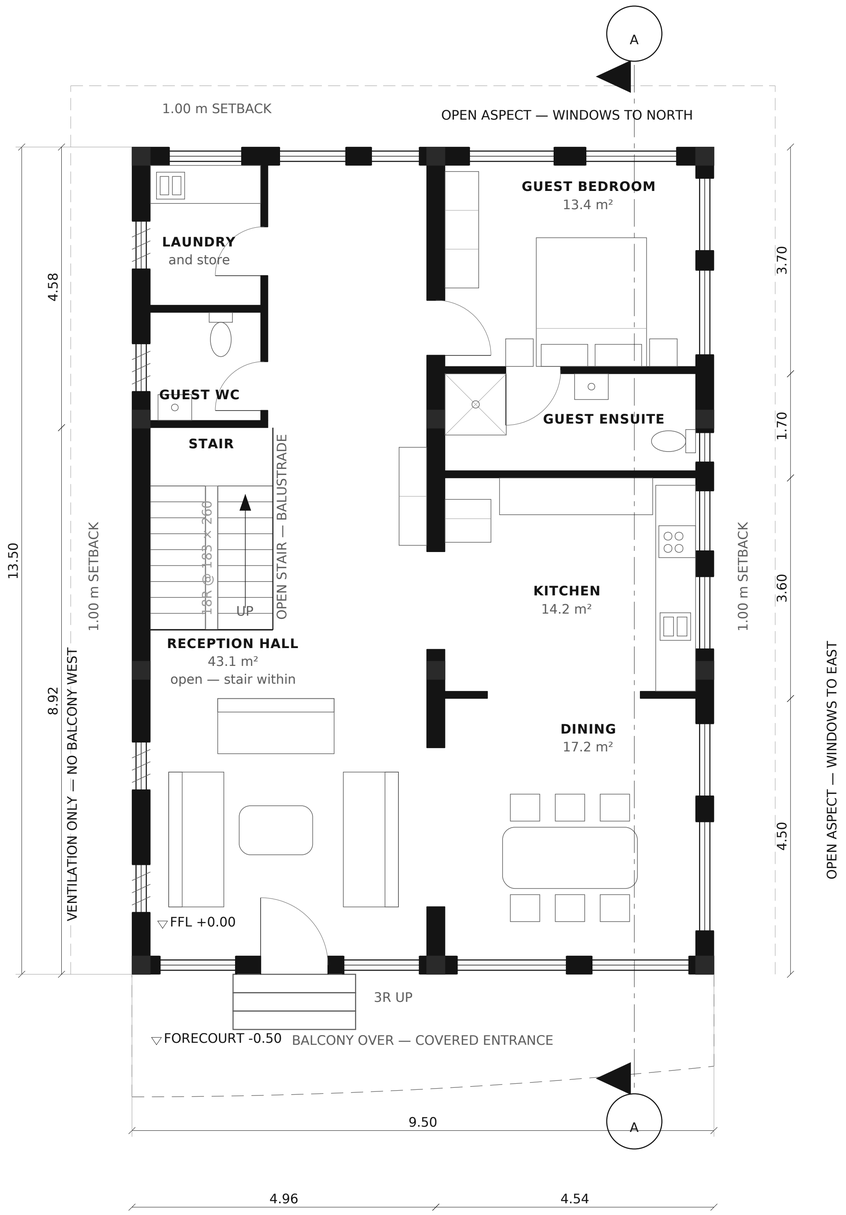

GRAPHIC SCALE 1:50

0 2 4 6 8 10 m

# GROUND FLOOR PLAN — DETACHED VILLA

LEVEL +0.00 · 1:50 @ A1 · METRES

## KEY

- Masonry wall cut by section — 200 mm partition, 300 mm external / party
- Internal stud or block partition, 120 mm
- Terrace parapet, 250 mm × 1100 mm high
- Single leaf door, swing shown to opening side
- Glazed opening — arched head where noted
- Element above the cut plane (pergola, slab over)
- Void / open to sky
- ▽ +0.00 — Finished floor level datum

## AREA SCHEDULE

| | |
|---|---|
| RECEPTION HALL | 43.1 m² |
| STAIR | 6.6 m² |
| GUEST WC | 3.2 m² |
| LAUNDRY | 4.1 m² |
| DINING | 17.2 m² |
| KITCHEN | 14.2 m² |
| GUEST ENSUITE | 6.5 m² |
| GUEST BEDROOM | 13.4 m² |
| **TOTAL** | **108.3 m²** |
| GROSS INTERNAL AREA, THIS FLOOR | 114.8 m² |
| BEDROOMS | 1 — the guest suite; 8 above |
| FLOOR ABOVE | +3.30 |

## GENERAL NOTES

1. Final draft — layout agreed. The floor you receive people on: the family living is upstairs where the balconies are, so this one takes arrival, eating and a guest suite for anyone who cannot manage the stair.

2. Hall, dining and kitchen are one open sequence. The spine is cased open to both at 2.60 and 1.60 m, and the kitchen serves the dining through a 2.50 m opening rather than a door. Only the guest suite and the two service rooms are closed.

3. The reception hall is the whole west strip at 43.1 m², with the stair standing in it. It turns the corner behind the stair and runs on to the north wall, so the guest bedroom opens off the hall and there is no circulation room anywhere on the floor.

4. Guest WC, laundry and store are one block against the west wall, the only part of this floor that is walled off. East and north carry ordinary windows, the west louvred ventilation only.

5. The front door is in the hall's south wall, under the cantilever, which projects about 1.75 m there — so the entrance is covered without a porch being added to the elevation. Three risers up from the forecourt at −0.50.

6. Bedrooms are numbered 1 to 11 through the house, south to north and west before east on each floor; the ground floor's room is the guest bedroom and carries no number.

7. The A-300 enlargements are the last sheets still on the old 11.50 × 14.50 footprint.

**FOUR-STOREY VACATION HOME** — PRIVATE CLIENT

DRAWING

**GROUND FLOOR PLAN — DETACHED VILLA**

| DRAWING No | REVISION | SCALE | DATE |
|---|---|---|---|
| **A-100** | **P14** | **1:50 @ A1** | **2026-10-07** |

Final draft — layout agreed with the client; not for construction.
Do not scale; work to figured dimensions only.

REVISIONS

P11 2026-10-07 penthouse: 2.51 m corridor outside the flat; living room to the face
P12 2026-10-07 bedrooms numbered 1-11; all five floors issued as final draft
P13 2026-10-07 site plan redrawn for the detached villa
P14 2026-10-07 section A-A recut through the east strip, and marked on every plan