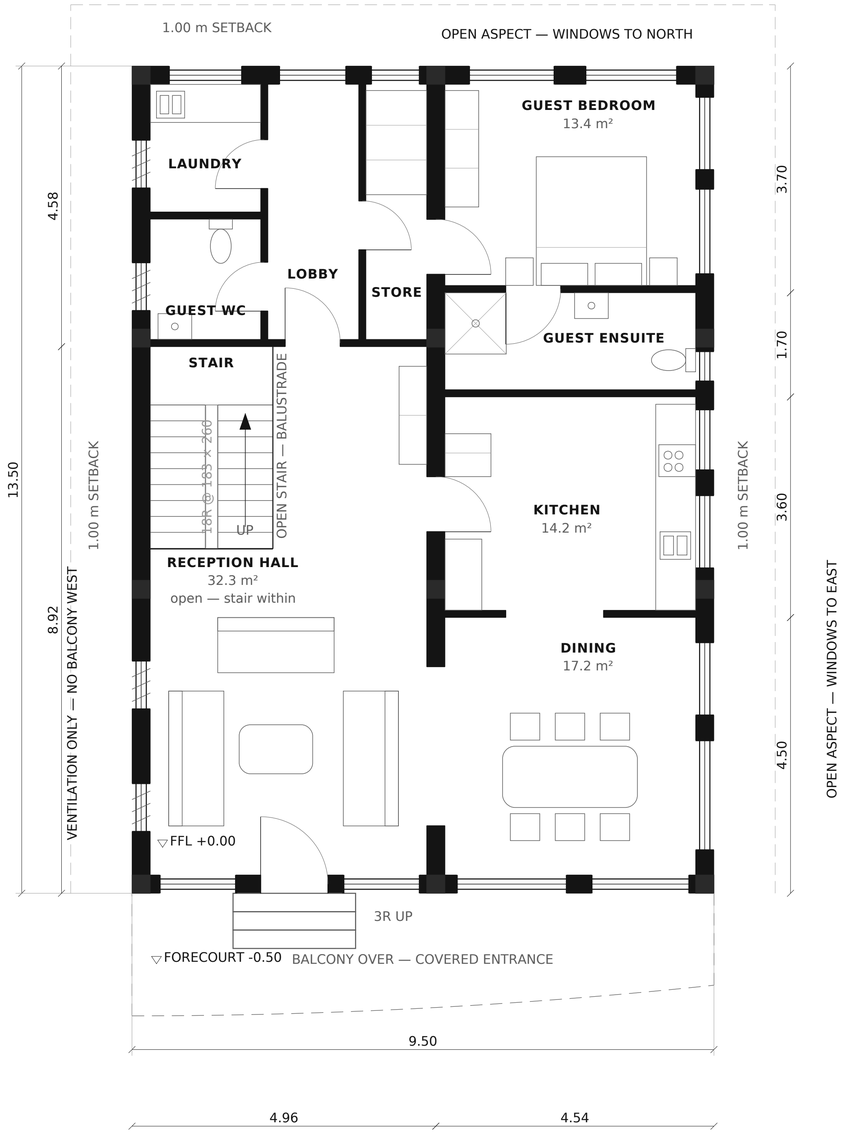

GRAPHIC SCALE 1:50

0 2 4 6 8 10 m

N

GROUND FLOOR PLAN — DETACHED VILLA

LEVEL +0.00 · 1:50 @ A1 · METRES

KEY

- Masonry wall cut by section — 200 mm partition, 300 mm external / party
- Internal stud or block partition, 120 mm
- Terrace parapet, 250 mm × 1100 mm high
- Single leaf door, swing shown to opening side
- Glazed opening — arched head where noted
- Element above the cut plane (pergola, slab over)
- Void / open to sky
- ▽ +0.00 Finished floor level datum

AREA SCHEDULE

RECEPTION HALL	32.3 m²
STAIR	6.6 m²
GUEST WC	3.5 m²
LAUNDRY	3.7 m²
LOBBY	6.2 m²
STORE	4.1 m²
DINING	17.2 m²
KITCHEN	14.2 m²
GUEST ENSUITE	6.5 m²
GUEST BEDROOM	13.4 m²
TOTAL	**107.7 m²**
GROSS INTERNAL AREA, THIS FLOOR	114.8 m²
BEDROOMS	1 — the guest suite; 8 above
FLOOR ABOVE	+3.30

GENERAL NOTES

1. Draft for comment. The floor you receive people on: the family living is upstairs where the balconies are, so this one takes arrival, eating and a guest suite for anyone who cannot manage the stair.

2. The west strip is the first and third floors' exactly — one open room from the south wall to the stair hall line, with the stair standing in it. Upstairs that room is the living area; here it is the reception hall at 32.3 m².

3. The front door is in its south wall, under the cantilever. The balcony projects about 1.75 m there, so the entrance is covered without a porch being added to the elevation. Three risers up from the forecourt at −0.50.

4. Dining and kitchen take the two south bands of the east strip, next to each other and linked by a cased opening; the guest suite has the quiet north-east corner on the north and east windows.

5. Guest WC, laundry and store fill the north-west behind the reception hall, off a lobby that also reaches the guest bedroom through the spine. East and north carry ordinary windows, the west louvred ventilation only.

6. The site plan and section A–A are still on the old 11.50 × 14.50 footprint.

FOUR-STOREY VACATION HOME — PRIVATE CLIENT

DRAWING

GROUND FLOOR PLAN — DETACHED VILLA

DRAWING No	REVISION	SCALE	DATE
A-100	**P7**	**1:50 @ A1**	**2026-10-06**

Preliminary design issue — not for construction.
Do not scale; work to figured dimensions only.

REVISIONS

P4 2026-09-29 north and east opened up, light court removed
P5 2026-10-06 detached villa: 1.00 m setbacks, wave cantilever
P6 2026-10-06 lobby opened, north hall merged into the bedroom
P7 2026-10-06 second floor agreed; ground floor redrawn as the villa