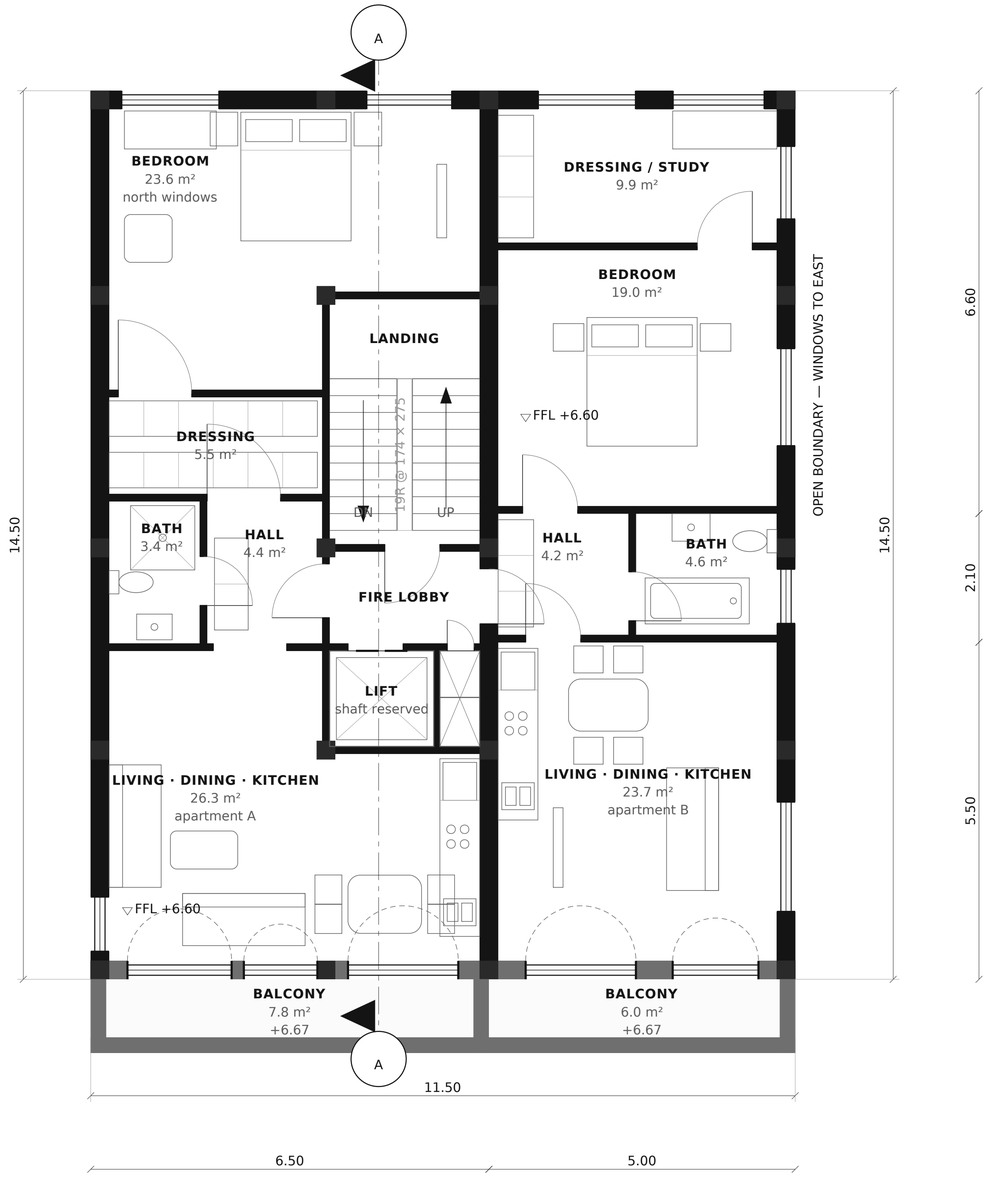

GRAPHIC SCALE 1:50

0 2 4 6 8 10 m

N

SECOND FLOOR PLAN

LEVEL +6.60 · 1:50 @ A1 · METRES

KEY

- Masonry wall cut by section — 200 mm partition, 300 mm external / party
- Internal stud or block partition, 120 mm
- Terrace parapet, 250 mm × 1100 mm high
- Single leaf door, swing shown to opening side
- Glazed opening — arched head where noted
- Element above the cut plane (pergola, slab over)
- Void / open to sky
- ▽ +0.00 — Finished floor level datum

AREA SCHEDULE

APT A LIVING / KITCHEN	26.3 m²
APT A BATHROOM	3.4 m²
APT A ENTRY HALL	4.4 m²
APT A DRESSING	5.5 m²
APT A BEDROOM	23.6 m²
LIFT SHAFT	2.7 m²
FIRE LOBBY	3.7 m²
PROTECTED STAIR	9.8 m²
APT B LIVING / KITCHEN	23.7 m²
APT B ENTRY HALL	4.2 m²
APT B BATHROOM	4.6 m²
APT B BEDROOM	19.0 m²
APT B DRESSING / STUDY	9.9 m²
TOTAL	**140.7 m²**
GROSS INTERNAL AREA, THIS FLOOR	147.3 m²
APARTMENT A / APARTMENT B	64.7 / 63.2 m²
BALCONY A / B (EXTERNAL)	7.8 / 6.0 m²

GENERAL NOTES

1. Two one-bedroom apartments off the protected fire lobby: apartment A occupies block A around the core, apartment B the whole of block B. Balconies run the full width of each block, cantilevered 1.20 m with a 1.10 m parapet.

2. Both units are planned open: living, dining and kitchenette read as one room with no corridor, and every other room — bathroom included — opens off the entry hall.

3. Wet rooms stack onto the party wall spine. The riser cupboard carrying the soil, water and extract risers is entered from the fire lobby, not from either apartment.

4. North and east are open boundaries. Block B is windowed on the east at every level and block A's bedroom takes two windows in the north wall, so every habitable room is daylit and naturally ventilated. The west wall is the only blind elevation.

5. Escape is by a single protected stair, adopted on the client's instruction: FD30S doors onto the fire lobby, sprinklers throughout. The stair has no external wall, so it is smoke-vented by a 1.2 m² automatic opening vent at its head — see A-103 and A-200. The governing code is still to be named and the strategy agreed.

FOUR-STOREY VACATION HOME — PRIVATE CLIENT

DRAWING

SECOND FLOOR PLAN

DRAWING No	REVISION	SCALE	DATE
A-102	**P4**	**1:50 @ A1**	**2026-09-29**

Preliminary design issue — not for construction.
Do not scale; work to figured dimensions only.

REVISIONS

- P1 2026-09-18 first issue
- P2 2026-09-24 east windows, taller floors, garden on A-100
- P3 2026-09-29 four storeys, apartments, straight north boundary
- P4 2026-09-29 north and east opened up, light court removed