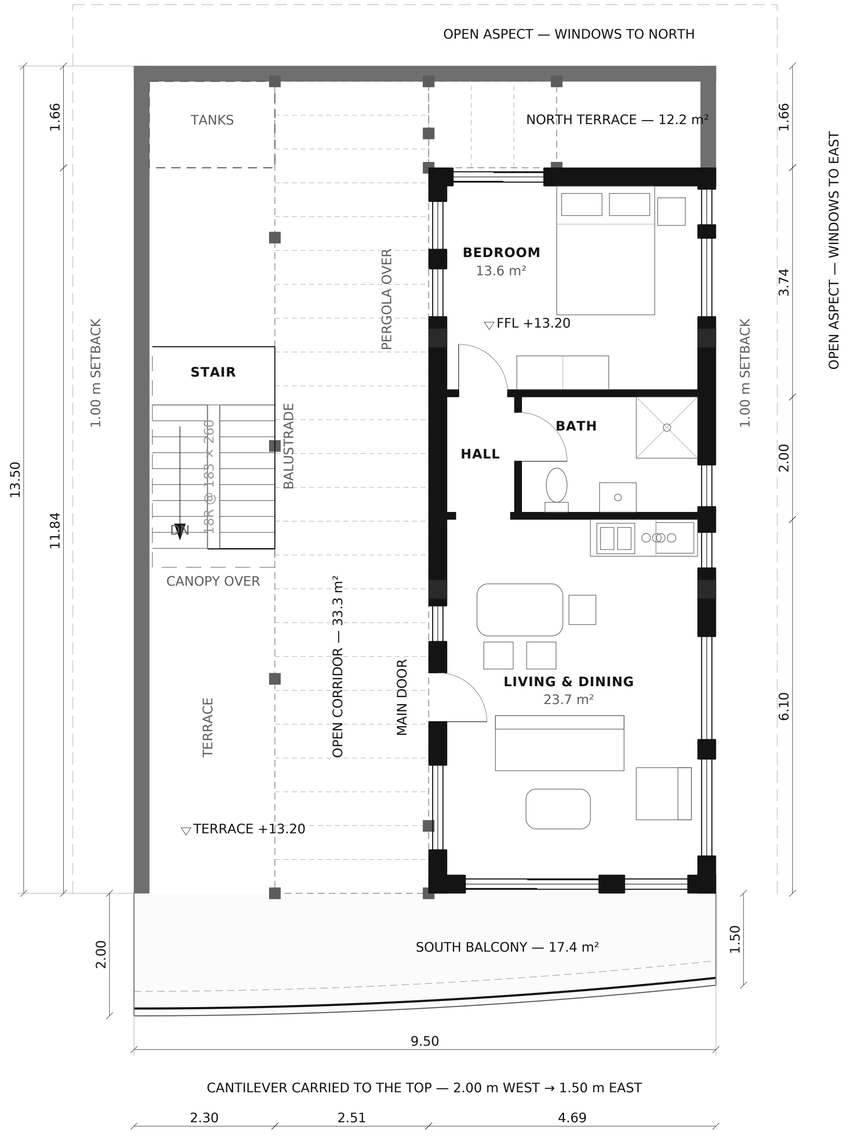

GRAPHIC SCALE 1:50

0 2 4 6 8 10 m

N

PENTHOUSE PLAN — DETACHED VILLA

LEVEL +13.20 · 1:50 @ A1 · METRES

KEY

- Masonry wall cut by section — 200 mm partition, 300 mm external / party
- Internal stud or block partition, 120 mm
- Terrace parapet, 250 mm × 1100 mm high
- Single leaf door, swing shown to opening side
- Glazed opening — arched head where noted
- Element above the cut plane (pergola, slab over)
- Void / open to sky
- ▽ +0.00 Finished floor level datum

AREA SCHEDULE

LIVING AND DINING	23.7 m²
HALL	2.1 m²
BATH	5.4 m²
BEDROOM	13.6 m²
TOTAL	**44.8 m²**
GROSS INTERNAL AREA, FLAT	46.0 m²
SOUTH BALCONY, ON THE CANTILEVER	17.4 m²
SOUTH TERRACE, WEST OF THE CORRIDOR	11.5 m²
NORTH TERRACE	12.2 m²
OPEN CORRIDOR	33.3 m²
TOP OF PENTHOUSE SLAB	+16.45
FLOOR BELOW	+9.90

GENERAL NOTES

1. Draft for comment. The two open areas are joined outside the flat, down the west side, by a corridor 2.51 m clear against the 2.00 m asked for, with the pergola running over its whole length. The front door is off it.

2. The living room runs south to the building's face, so it opens straight onto the cantilever the way every floor below does. That wall is the best-founded in the flat: y 3.65 is a grid line, so it sits on the columns at x 17.46 and 21.85 and over the external wall below.

3. 46.0 m² indoors; 17.4 m² of balcony on the cantilever, 11.5 m² of terrace beside the stair, 12.2 m² north and 33.3 m² of corridor. All four run into one another.

4. The corridor passes east of the stair, not west: the well is 2.00 m wide and hard against the west parapet, and its half landing is 1.65 m below this floor, so it stays open. Its east side is the flat's west wall, on the spine at x 17.46 - the one line on this side of the roof with a beam under it.

5. That leaves the flat 4.09 m clear, which will not take two bedrooms side by side: stacking them needs 12.06 m of the 13.50 m depth and leaves 1.44 m for both terraces. The second bedroom is what pays for the corridor.

6. Nothing is built over the cantilever - it carries its parapet and no more. At +16.45 the penthouse is a fourth storey for most planning codes. The site plan, section A—A and the A-300 enlargements are still on the old 11.50 × 14.50 footprint.

FOUR-STOREY VACATION HOME — PRIVATE CLIENT

DRAWING

PENTHOUSE PLAN — DETACHED VILLA

DRAWING No	REVISION	SCALE	DATE
A-104	**P11**	**1:50 @ A1**	**2026-10-07**

Preliminary design issue — not for construction.
Do not scale; work to figured dimensions only.

REVISIONS

P8 2026-10-06 ground floor opened up; guest room off the hall
P9 2026-10-06 penthouse added: two-bedroom roof apartment
P10 2026-10-07 penthouse between two terraces, pergola joining them
P11 2026-10-07 penthouse: 2.51 m corridor outside the flat, west side