THIRD FLOOR PLAN — DETACHED VILLA

LEVEL +9.90 · 1:50 @ A1 · METRES

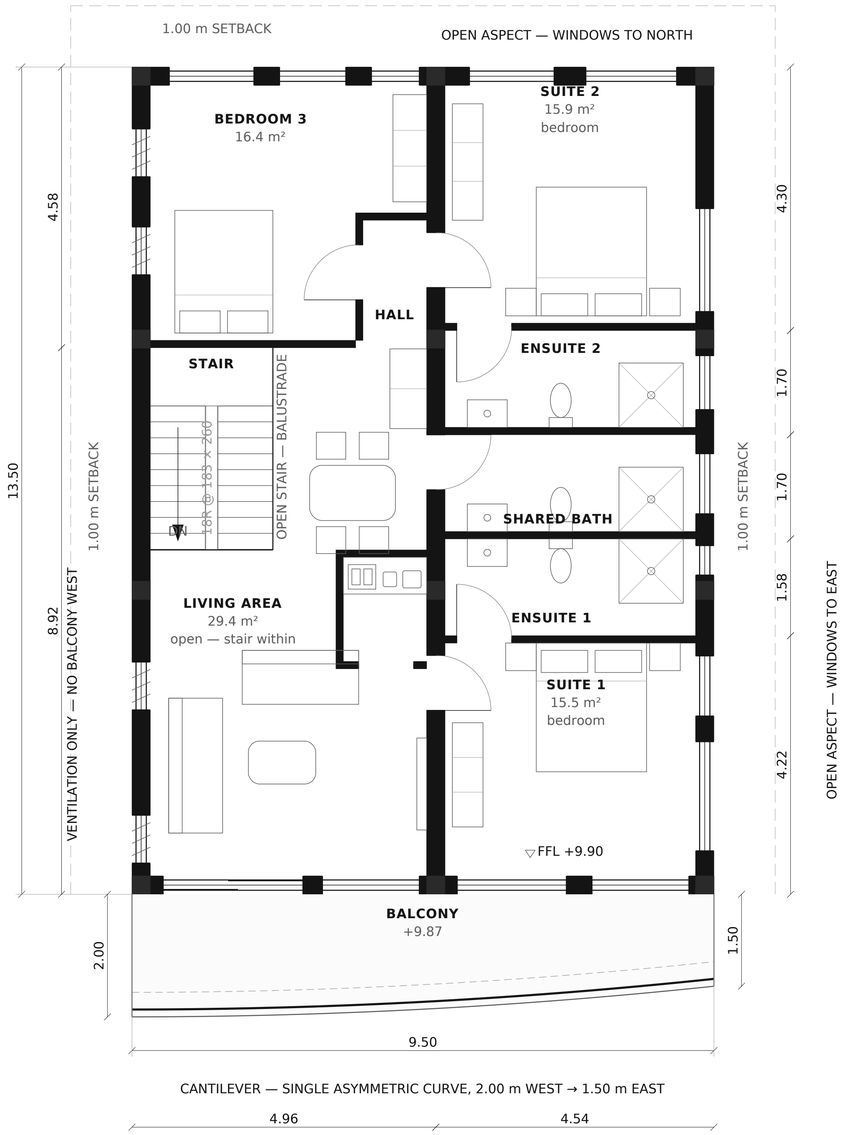

GRAPHIC SCALE 1:50

0 2 4 6 8 10 m

KEY

- Masonry wall cut by section — 200 mm partition, 300 mm external / party
- Internal stud or block partition, 120 mm
- Terrace parapet, 250 mm × 1100 mm high
- Single leaf door, swing shown to opening side
- Glazed opening — arched head where noted
- Element above the cut plane (pergola, slab over)
- Void / open to sky
- ▽ +0.00 Finished floor level datum

AREA SCHEDULE

LIVING AREA	29.4 m²
STAIR	6.6 m²
HALL	2.0 m²
SUITE 1 BEDROOM	15.5 m²
SUITE 1 ENSUITE	6.5 m²
SHARED BATH	6.5 m²
SUITE 2 ENSUITE	6.5 m²
SUITE 2 BEDROOM	15.9 m²
BEDROOM 3	16.4 m²
TOTAL	**105.3 m²**
GROSS INTERNAL AREA, THIS FLOOR	114.8 m²
BALCONY, EXTERNAL	17.4 m²
ROOF OVER, TOP OF SLAB	+13.20

GENERAL NOTES

1. Final draft — layout agreed. The building is set back 1.00 m from the west, north and east boundaries; the south faces the street across our own forecourt. Detaching costs 22% of the floor — 114.8 m² against 147.3 — and removes the party wall, so one structural spine divides the plate.

2. The west strip south of bedroom 3 is one room: no wall divides the living area from the stair standing in it, and the pantry is its only enclosure. The stair is a private villa stair — 900 mm flights, 18R at 183 × 260, landing 950 mm — needing no enclosure, no smoke vent and no lift.

3. The south cantilever is reinforced concrete: one asymmetric curve bowed outward, 2.00 m at the west end sweeping away to 1.50 m at the east. Every point on the edge stands outside the line joining the two ends.

4. East and north carry ordinary windows; both neighbours are 3.00 m high. The west carries louvred ventilation only.

5. Suite 1 and the shared bath open off the living area; suite 2 and bedroom 3 off the hall, which stops once it has served those two doors — the 2.08 m of dead end beyond goes to bedroom 3, which turns the corner behind it at 16.4 m².

6. Suite 2 has no balcony: its bedroom takes the north wall and two windows instead. Floors 0–2, the site plan and section A-A are still on the old 11.50 × 14.50 footprint.

FOUR-STOREY VACATION HOME — PRIVATE CLIENT

DRAWING

THIRD FLOOR PLAN — DETACHED VILLA

DRAWING No	REVISION	SCALE	DATE
A-103	**P6**	**1:50 @ A1**	**2026-10-06**

Final draft — layout agreed with the client; not for construction.
Do not scale; work to figured dimensions only.

REVISIONS

- P1 2026-09-18 first issue
- P2 2026-09-24 east windows, taller floors, garden on A-100
- P3 2026-09-29 four storeys, apartments, straight north boundary
- P4 2026-09-29 north and east opened up, light court removed
- P5 2026-10-06 detached villa: 1.00 m setbacks, wave cantilever
- P6 2026-10-06 lobby opened, north hall merged into the bedroom