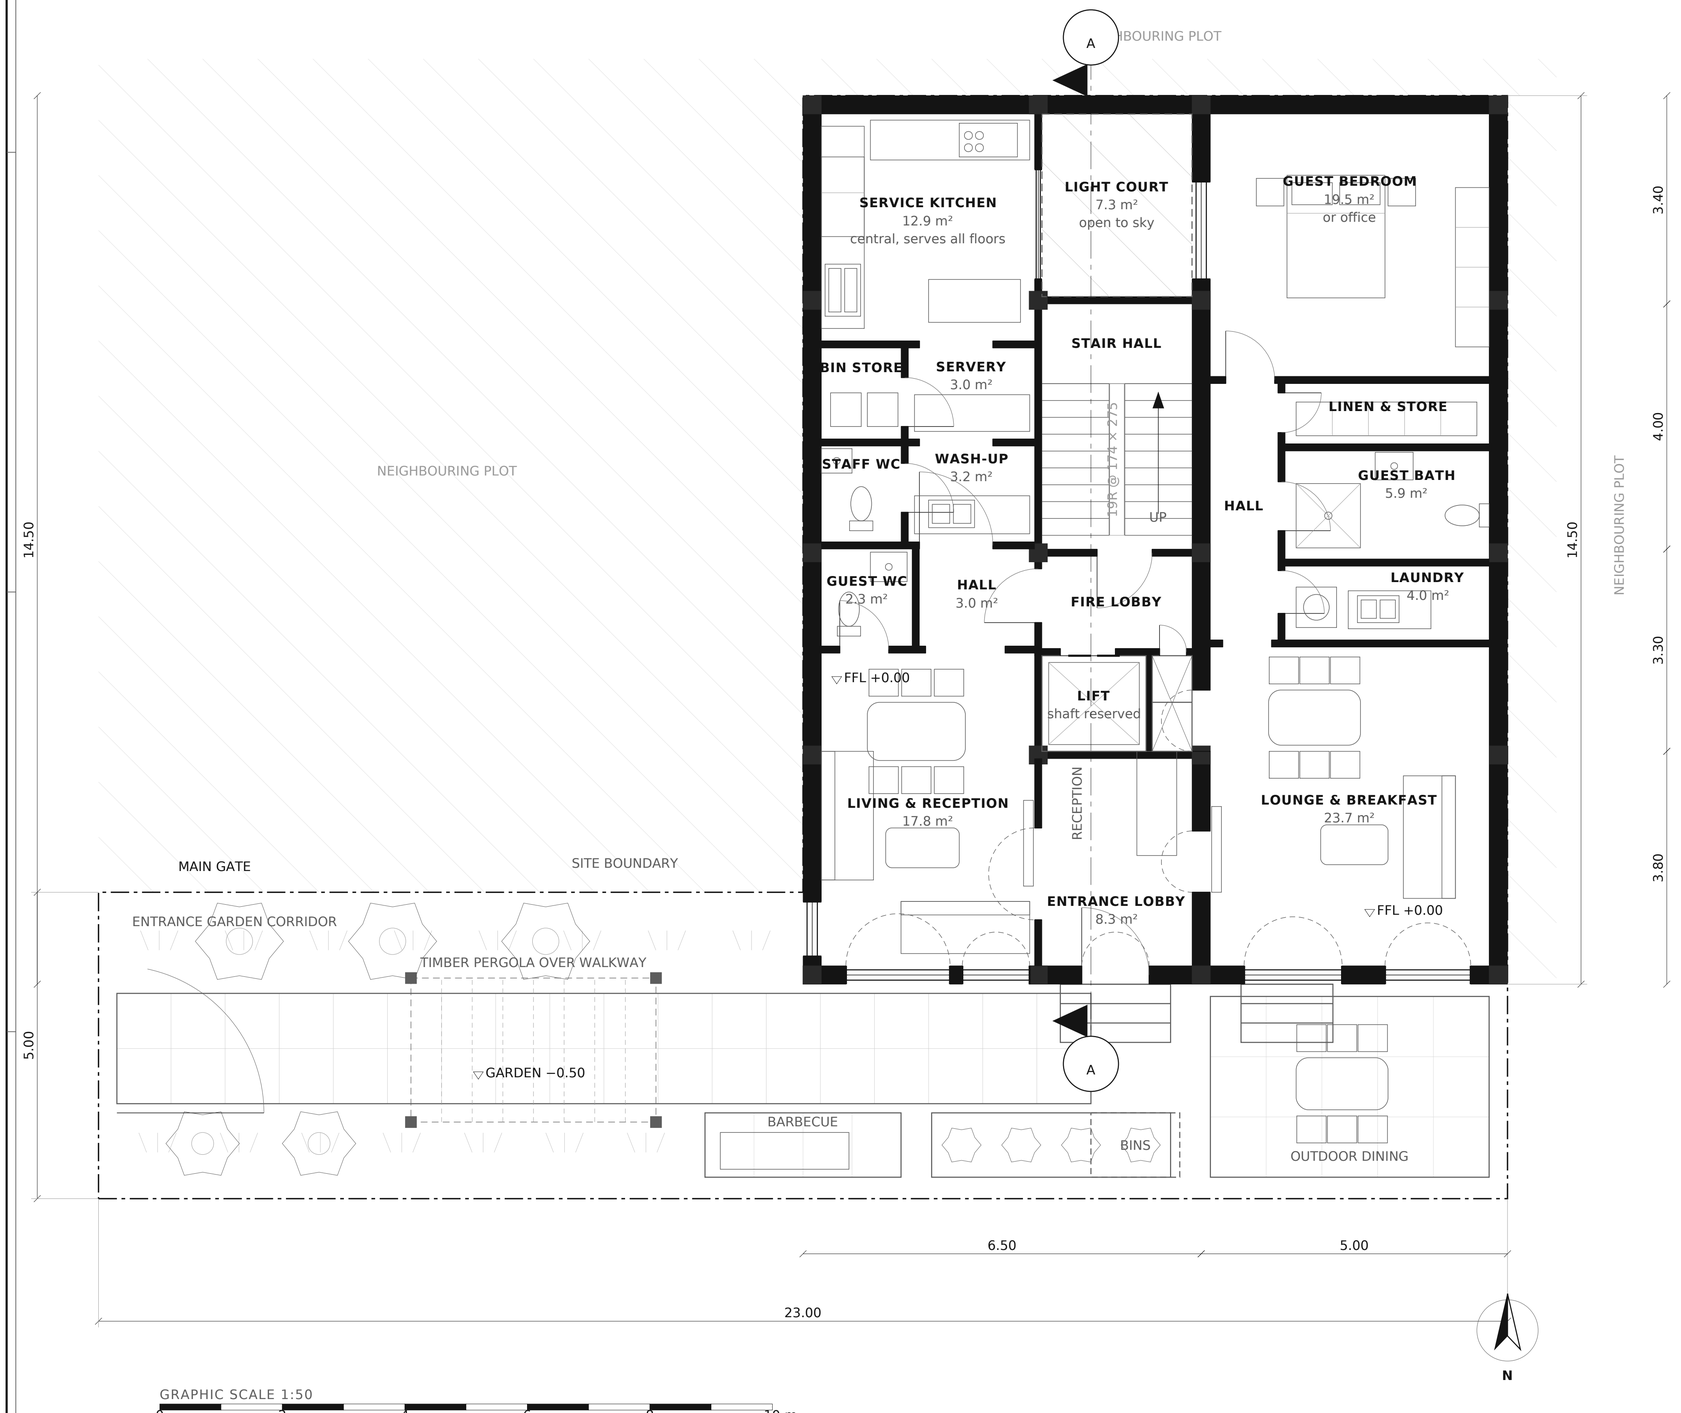

GROUND FLOOR PLAN

LEVEL +0.00 · 1:50 @ A1 · METRES

KEY

- Masonry wall cut by section — 200 mm partition, 300 mm external / party
- Internal stud or block partition, 120 mm
- Terrace parapet, 250 mm × 1100 mm high
- Single leaf door, swing shown to opening side
- Glazed opening — arched head where noted
- Element above the cut plane (pergola, slab over)
- Void / open to sky
- ▽ +0.00 — Finished floor level datum

AREA SCHEDULE

ENTRANCE LOBBY & RECEPTION	8.3 m²
LIVING & RECEPTION	17.8 m²
GUEST WC	2.3 m²
HALL	3.0 m²
STAFF WC	2.0 m²
WASH-UP	3.2 m²
BIN STORE	1.9 m²
SERVERY	3.0 m²
SERVICE KITCHEN	12.9 m²
LIFT SHAFT	2.7 m²
FIRE LOBBY	3.7 m²
PROTECTED STAIR	9.8 m²
LOUNGE & BREAKFAST	23.7 m²
HALL, BLOCK B	4.6 m²
CENTRAL LAUNDRY	4.0 m²
GUEST BATH	5.9 m²
LINEN & STORE	3.3 m²
GUEST BEDROOM	19.5 m²
TOTAL	**131.5 m²**
GROSS INTERNAL AREA, THIS FLOOR	140.0 m²
LIGHT COURT, OPEN TO SKY	7.3 m²
SLAB TO SLAB	3.30 m · 3.00 m clear

GENERAL NOTES

1. This floor is one non-residential compartment under the apartments: 2 hour separation to the floor over, sprinklered, with a suppression hood over the cooking line.

2. The 12.9 m² service kitchen and the 4.0 m² laundry serve all four storeys, reached through the servery and the block B hall so that no room is entered through another. Kitchen extract rises in a fire-rated shaft off the fire lobby, discharging above roof level.

3. Living, reception, entrance lobby and lounge read as one sequence through 1.00 m arched openings in the party wall. The guest WC opens off the reception and the guest bath off the block B hall, neither on the service route.

4. The east boundary wall is solid here — the adjoining owner may build up to 3.00 m against it — so the kitchen and guest bedroom are daylit from the light court. Internal rooms are extracted at six air changes per hour.

FOUR-STOREY VACATION HOME — PRIVATE CLIENT

DRAWING

GROUND FLOOR PLAN

DRAWING No	REVISION	SCALE	DATE
A-100	**P3**	**1:50 @ A1**	**2026-09-29**

Preliminary design issue — not for construction.
Do not scale; work to figured dimensions only.

REVISIONS
P1 2026-09-18 first issue
P2 2026-09-24 east windows, taller floors, garden on A-100
P3 2026-09-29 four storeys, apartments, straight north boundary