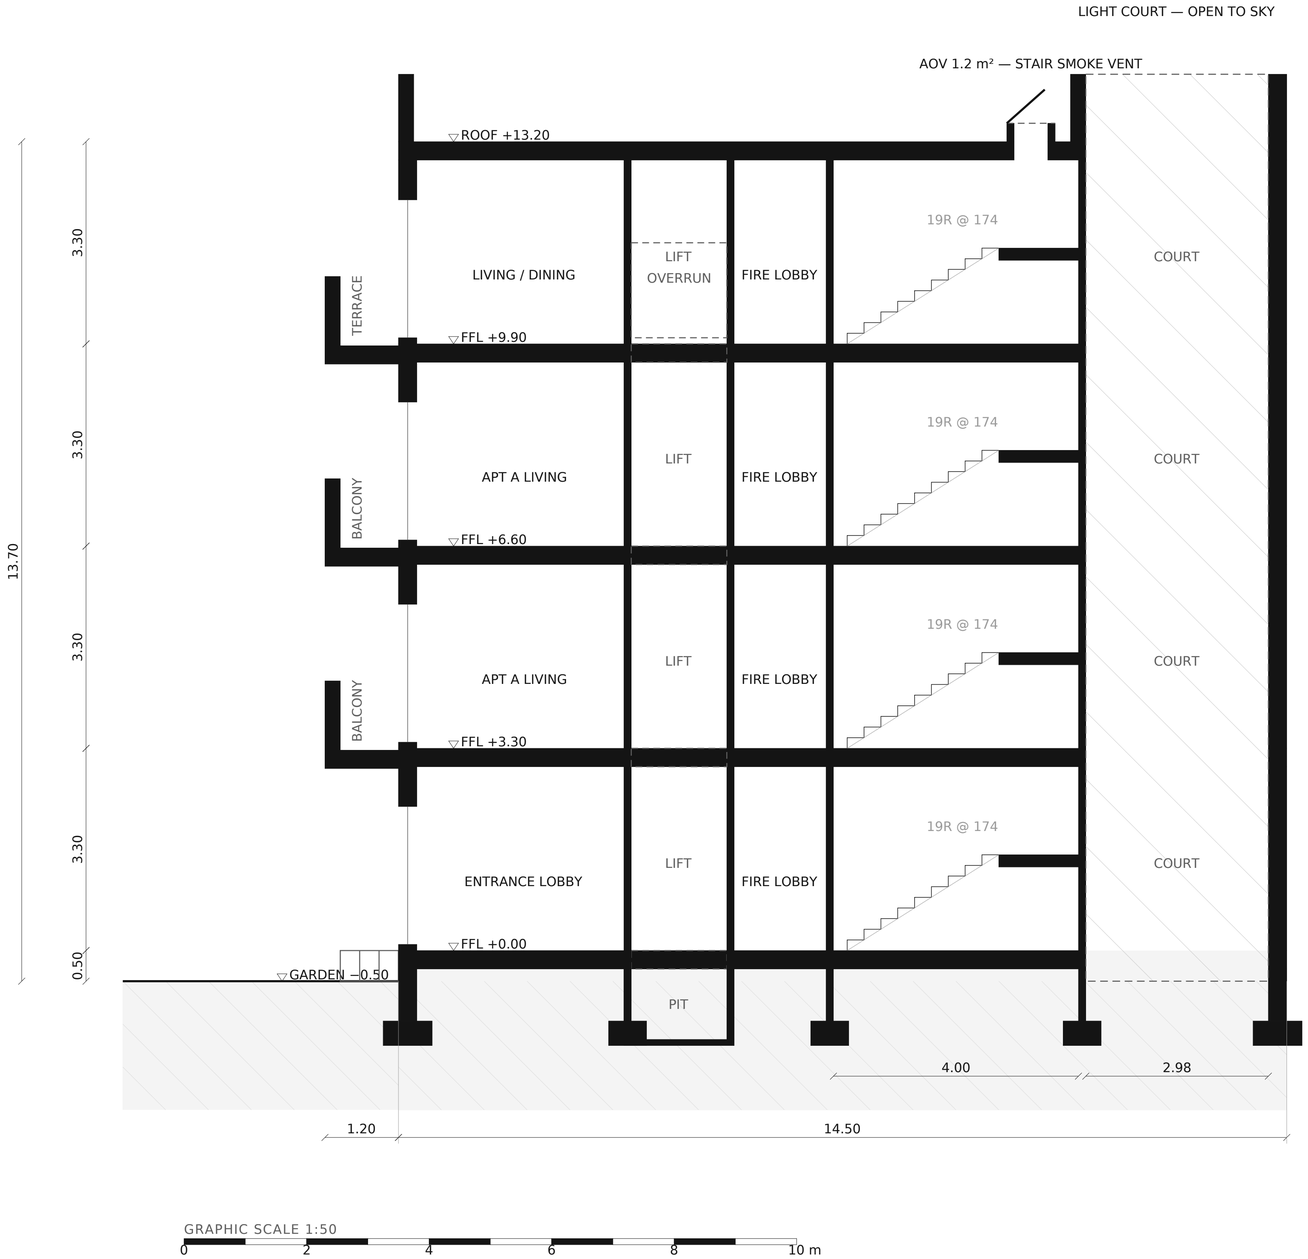

GRAPHIC SCALE 1:50

0 2 4 6 8 10 m

SECTION A–A

LEVEL through the core · 1:50 @ A1 · METRES

KEY

- Masonry wall cut by section — 200 mm partition, 300 mm external / party
- Internal stud or block partition, 120 mm
- Terrace parapet, 250 mm × 1100 mm high
- Single leaf door, swing shown to opening side
- Glazed opening — arched head where noted
- Element above the cut plane (pergola, slab over)
- Void / open to sky
- ▽ +0.00 — Finished floor level datum

LEVEL DATUMS

GARDEN	-0.50
GROUND FLOOR	+0.00
FIRST FLOOR	+3.30
SECOND FLOOR	+6.60
THIRD FLOOR	+9.90
ROOF, TOP OF SLAB	+13.20
CLEAR CEILING HEIGHT	3.00 m
STRUCTURAL ZONE	0.30 m
OVERALL, GARDEN TO ROOF	13.70 m

GENERAL NOTES

1. Section looking west, cut on the line marked A–A on the floor plans: through the south glazing, the lift shaft, the protected lobby, the stair and the light court.

2. The light court is open to sky for the full height of the building and is the daylight and stack ventilation source for the centre of the plan, where the boundaries are blind.

3. The lift shaft is built full height with removable infill slabs at each level, shown dashed, so a lift can be installed later without cutting structure. Pit and overrun are indicative and to be confirmed against the chosen lift.

4. Flat slab on the column grid, 300 mm structural zone, giving 3.00 m clear at every level and 3.30 m floor to floor.

5. The stair is enclosed in the middle of block A and has no external wall, so it is smoke-vented at its head by a 1.2 m² automatic opening vent through the roof slab, shown open. The single-stair strategy is the client's decision and still needs the authority's agreement.

6. Foundations are shown indicatively only and are subject to a ground investigation and the engineer's design.

FOUR-STOREY VACATION HOME — PRIVATE CLIENT

DRAWING

SECTION A–A

DRAWING No	REVISION	SCALE	DATE
A-200	**P3**	**1:50 @ A1**	**2026-09-29**

Preliminary design issue — not for construction.
Do not scale; work to figured dimensions only.

REVISIONS
P1 2026-09-18 first issue
P2 2026-09-24 east windows, taller floors, garden on A-100
P3 2026-09-29 four storeys, apartments, straight north boundary