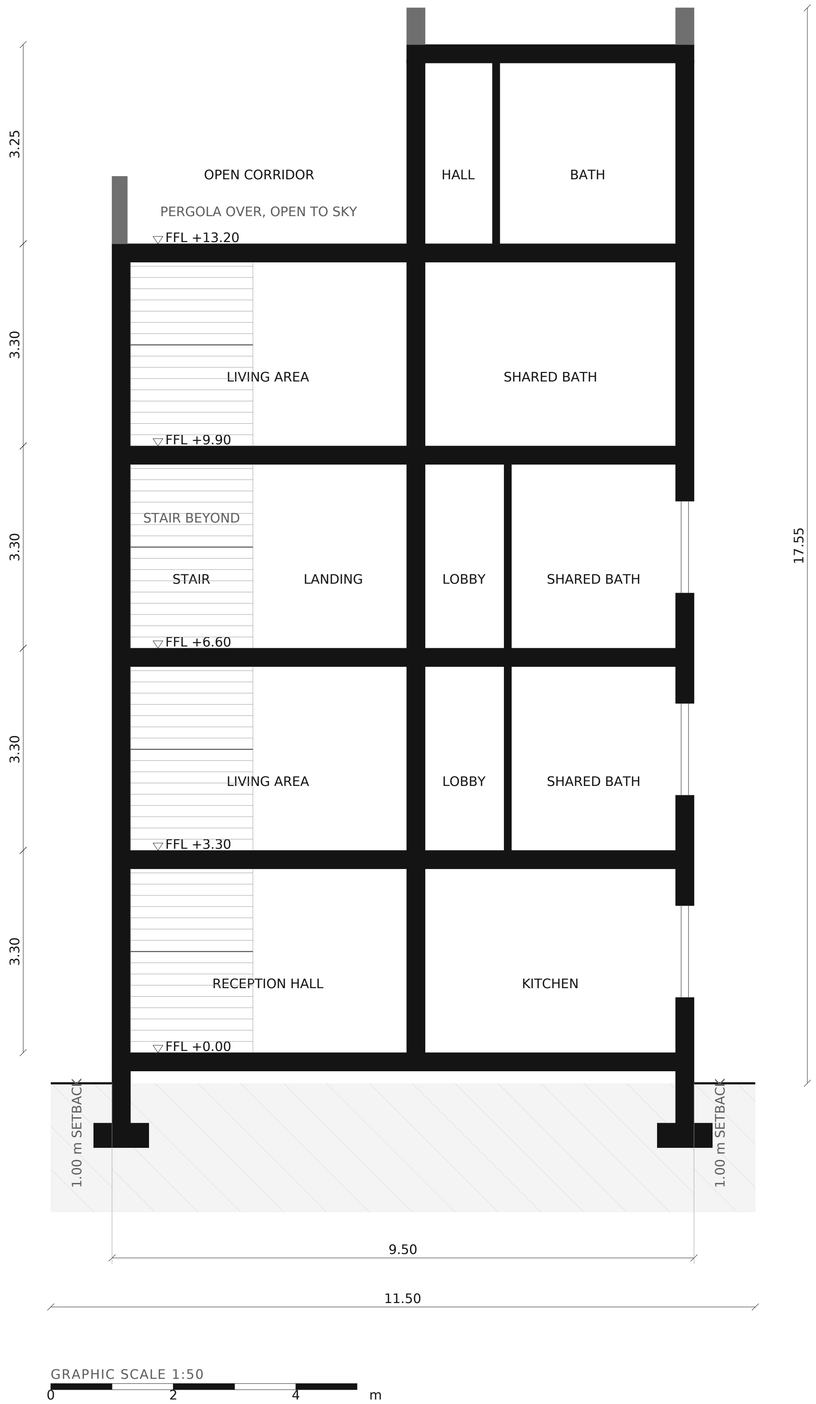


# SECTION B–B — TRANSVERSE

LEVEL looking north · 1:50 @ A1 · METRES

## KEY

- External / party wall cut by section, 300 mm — brick, colour unrestricted
- Internal partition, 100 mm — red brick
- Terrace parapet, 250 mm × 1100 mm high
- Single leaf door, swing shown to opening side
- Glazed opening — arched head where noted
- Element above the cut plane (pergola, slab over)
- Void / open to sky
- ▽ +0.00 — Finished floor level datum

## THE CUT

| | |
|---|---|
| SECTION LINE | y = 10.80, looking north |
| WIDTH BETWEEN SETBACKS | 9.50 m |
| STRUCTURAL SPINE | x 17.31 – 17.61 |
| FLOOR TO FLOOR | 3.30 m |
| CLEAR HEIGHT | 3.00 m |
| STRUCTURAL ZONE | 300 mm |
| TOP OF BUILDING | +17.05 |
| EAST GLAZED AT THIS CUT | levels 0, 1 and 2 |

## GENERAL NOTES

1. Cut at y = 10.80, inside the stair well and clear of every cross wall, looking north. A-A cuts the other way and shows the depth; this is the only drawing of the width.

2. What the cut passes through was read off the plans by the probe in checks.py, not written from memory, and whether the east wall is glazed at the cut is worked out from the plan's own opening list each time the sheet is built.

3. The east wall is glazed on the lower three floors and solid on the third, which is the plans' arrangement and not a drafting choice. It can be glazed at all because the neighbour a metre east is a single storey.

4. The stair is beyond the cut, not in it: its flights run north-south, so this section crosses them end-on and they are drawn in thin line as seen through the open well.

5. At the penthouse the west half of the plate is the open corridor, outside the flat and open to the sky under its pergola. Foundations are indicative pending GEO-001.

**FIVE-STOREY VACATION VILLA** — SHAMANDEEL, QUESNA, MENOUFIA, EGYPT

DRAWING

**SECTION B–B — TRANSVERSE**

| DRAWING No | REVISION | SCALE | DATE |
|---|---|---|---|
| **ARC-301** | **P21** | **1:50 @ A1** | **2026-10-11** |

Preliminary design issue — not for construction.
Do not scale; work to figured dimensions only.

REVISIONS

P18 2026-10-07 scheme A adopted: serpentine balcony on every plan; site named
P19 2026-10-07 serpentine waist deepened 0.75 to 1.35 m; 15.7 m² of balcony a floor
P20 2026-10-07 internal partitions 100 mm red brick, specified by the client
P21 2026-10-07 300 mm external and party walls: brick, colour unrestricted