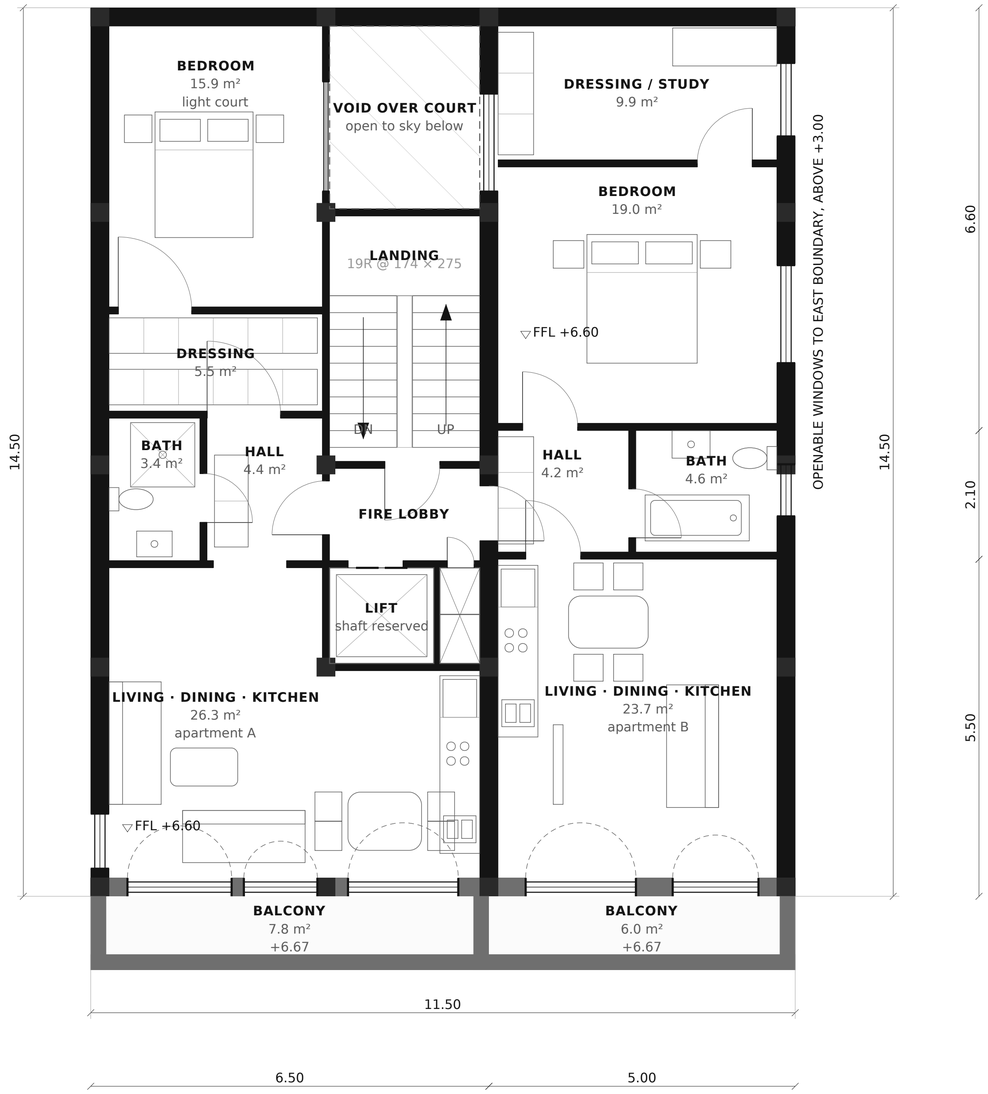

GRAPHIC SCALE 1:50

0 2 4 6 8 10 m

N

SECOND FLOOR PLAN

LEVEL +6.60 · 1:50 @ A1 · METRES

KEY

- Masonry wall cut by section — 200 mm partition, 300 mm external / party
- Internal stud or block partition, 120 mm
- Terrace parapet, 250 mm × 1100 mm high
- Single leaf door, swing shown to opening side
- Glazed opening — arched head where noted
- Element above the cut plane (pergola, slab over)
- Void / open to sky
- ▽ +0.00 Finished floor level datum

AREA SCHEDULE

APT A LIVING / KITCHEN	26.3 m²
APT A BATHROOM	3.4 m²
APT A ENTRY HALL	4.4 m²
APT A DRESSING	5.5 m²
APT A BEDROOM	15.9 m²
LIFT SHAFT	2.7 m²
FIRE LOBBY	3.7 m²
PROTECTED STAIR	9.8 m²
APT B LIVING / KITCHEN	23.7 m²
APT B ENTRY HALL	4.2 m²
APT B BATHROOM	4.6 m²
APT B BEDROOM	19.0 m²
APT B DRESSING / STUDY	9.9 m²
TOTAL	**133.0 m²**
GROSS INTERNAL AREA, THIS FLOOR	140.0 m²
APARTMENT A / APARTMENT B	57.1 / 63.3 m²
BALCONY A / B (EXTERNAL)	7.8 / 6.0 m²

GENERAL NOTES

1. Two one-bedroom apartments, both entered off the protected fire lobby: apartment A occupies block A around the core, apartment B the whole of block B.

2. Both units are planned open: living, dining and kitchenette read as one room with no corridor, and every other room — bathroom included — opens off the entry hall. Kitchenettes are a single joinery run against the party wall.

3. Wet rooms stack floor to floor onto the party wall spine. The riser cupboard carrying the soil, water and extract risers is entered from the fire lobby, not from either apartment; apartment A's kitchenette drains east to it in the floor zone.

4. East boundary openings: the adjoining plot is limited to 3.00 m in height, so the east wall is opened above that level and apartment B's bathroom is naturally ventilated. Openings in a boundary wall are subject to local fire separation and rights of light rules; confirm before construction.

5. Balconies run the full width of each block, cantilevered 1.20 m with a 1.10 m parapet. Escape is by the single protected stair, FD30S doors onto the lobby, sprinklers throughout — a proposal, to be verified against the governing code.

FOUR-STOREY VACATION HOME — PRIVATE CLIENT

DRAWING

SECOND FLOOR PLAN

DRAWING No	REVISION	SCALE	DATE
A-102	**P3**	**1:50 @ A1**	**2026-09-29**

Preliminary design issue — not for construction.
Do not scale; work to figured dimensions only.

REVISIONS
P1 2026-09-18 first issue
P2 2026-09-24 east windows, taller floors, garden on A-100
P3 2026-09-29 four storeys, apartments, straight north boundary