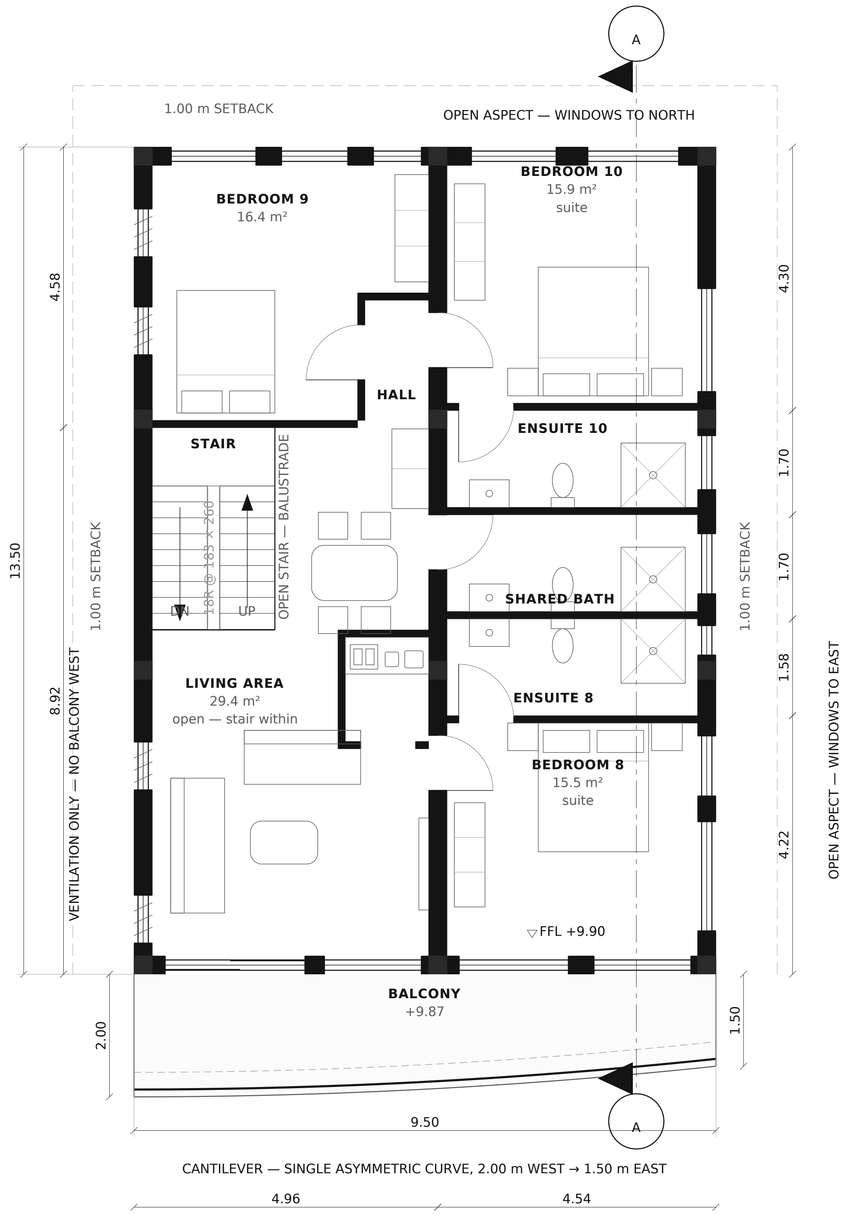


GRAPHIC SCALE 1:50

0 2 4 6 8 10 m

N

# THIRD FLOOR PLAN — DETACHED VILLA

LEVEL +9.90 · 1:50 @ A1 · METRES

## KEY

- Masonry wall cut by section — 200 mm partition, 300 mm external / party
- Internal stud or block partition, 120 mm
- Terrace parapet, 250 mm × 1100 mm high
- Single leaf door, swing shown to opening side
- Glazed opening — arched head where noted
- Element above the cut plane (pergola, slab over)
- Void / open to sky
- ▽ +0.00 — Finished floor level datum

## AREA SCHEDULE

| | |
|---|---|
| LIVING AREA | 29.4 m² |
| STAIR | 6.6 m² |
| HALL | 2.0 m² |
| BEDROOM 8 — SUITE | 15.5 m² |
| BEDROOM 8 ENSUITE | 6.5 m² |
| SHARED BATH | 6.5 m² |
| BEDROOM 10 ENSUITE | 6.5 m² |
| BEDROOM 10 — SUITE | 15.9 m² |
| BEDROOM 9 | 16.4 m² |
| **TOTAL** | **105.3 m²** |
| GROSS INTERNAL AREA, THIS FLOOR | 114.8 m² |
| BALCONY, EXTERNAL | 17.4 m² |
| ROOF OVER, TOP OF SLAB | +13.20 |

## GENERAL NOTES

1. Final draft — layout agreed. The building is set back 1.00 m from the west, north and east boundaries; the south faces the street across our own forecourt. Detaching costs 22% of the floor — 114.8 m² against 147.3 — and removes the party wall, so one structural spine divides the plate.

2. Bedrooms are numbered 1 to 11 through the house, south to north and west before east on each floor; the ground floor's room is the guest bedroom and carries no number.

3. The west strip south of bedroom 9 is one room: no wall divides the living area from the stair standing in it, and the pantry is its only enclosure. The stair is a private villa stair — 900 mm flights, 18R at 183 × 260, landing 950 mm — needing no enclosure, no smoke vent and no lift.

4. The south cantilever is reinforced concrete: one asymmetric curve bowed outward, 2.00 m at the west end sweeping away to 1.50 m at the east. Every point on the edge stands outside the line joining the two ends.

5. East and north carry ordinary windows; both neighbours are 3.00 m high. The west carries louvred ventilation only.

6. Bedroom 8 and the shared bath open off the living area; bedrooms 9 and 10 off the hall, which stops once it has served those two doors — the 2.08 m of dead end beyond goes to bedroom 9, which turns the corner behind it at 16.4 m². Bedroom 10 has no balcony: it takes the north wall and two windows instead.

**FOUR-STOREY VACATION HOME** — PRIVATE CLIENT

DRAWING

**THIRD FLOOR PLAN — DETACHED VILLA**

| DRAWING No | REVISION | SCALE | DATE |
|---|---|---|---|
| **A-103** | **P14** | **1:50 @ A1** | **2026-10-07** |

Final draft — layout agreed with the client; not for construction.
Do not scale; work to figured dimensions only.

REVISIONS

P11 2026-10-07 penthouse: 2.51 m corridor outside the flat; living room to the face
P12 2026-10-07 bedrooms numbered 1-11; all five floors issued as final draft
P13 2026-10-07 site plan redrawn for the detached villa
P14 2026-10-07 section A-A recut through the east strip, and marked on every plan