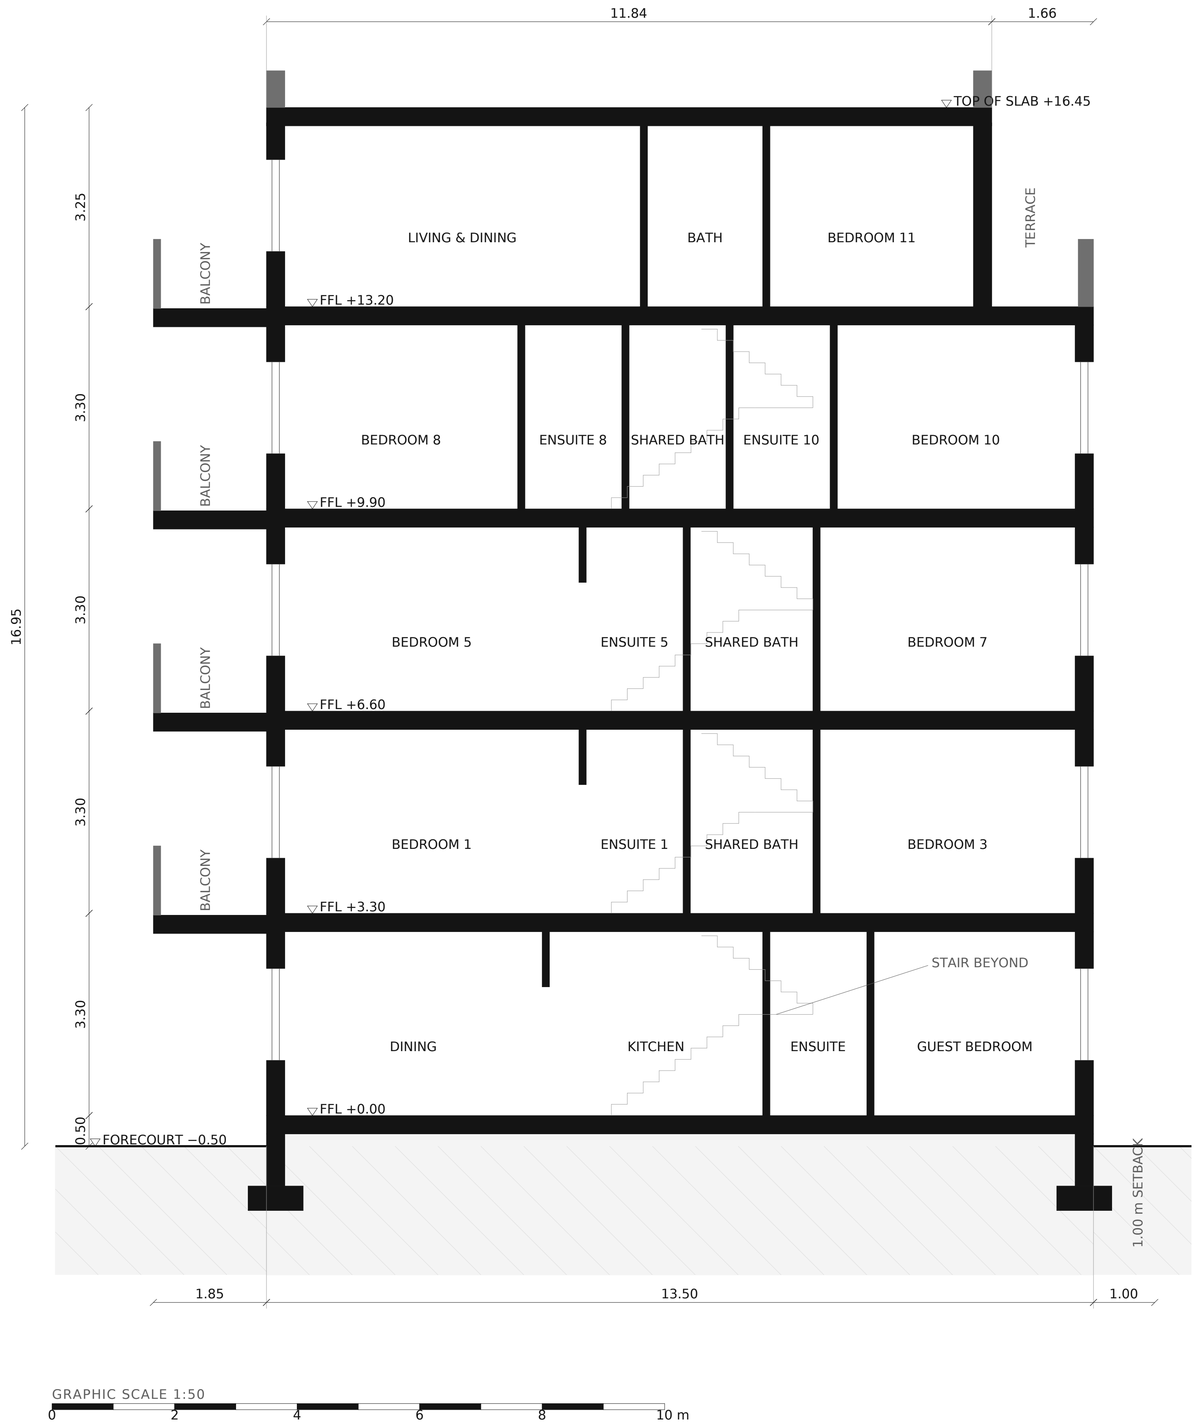


# SECTION A–A — DETACHED VILLA

LEVEL looking west · 1:50 @ A1 · METRES

## KEY

- External / party wall cut by section, 300 mm — brick, colour unrestricted
- Internal partition, 100 mm — red brick
- Terrace parapet, 250 mm × 1100 mm high
- Single leaf door, swing shown to opening side
- Glazed opening — arched head where noted
- Element above the cut plane (pergola, slab over)
- Void / open to sky
- ▽ +0.00 — Finished floor level datum

## LEVEL DATUMS

| | |
|---|---|
| FORECOURT AND GARDEN | -0.50 |
| GROUND FLOOR | +0.00 |
| FIRST FLOOR | +3.30 |
| SECOND FLOOR | +6.60 |
| THIRD FLOOR | +9.90 |
| PENTHOUSE FLOOR | +13.20 |
| PENTHOUSE, TOP OF SLAB | +16.45 |
| CLEAR CEILING HEIGHT | 3.00 m |
| STRUCTURAL ZONE | 0.30 m |
| OVERALL, GARDEN TO TOP | 16.95 m |

## GENERAL NOTES

1. Final draft — layout agreed. Looking west, cut on the line marked A–A on every plan, at x 20.70. That line is not arbitrary: it is the one north-south cut that passes through a room at every level and through every wet room in the east strip, and it clears all three column lines, so the slabs are seen spanning rather than a column standing in the cut.

2. The wet rooms on the first and second floors sit one over the other, wall for wall — 8.60, 10.30 and 12.42 on both — so each drops a single drainage stack straight to the ground. The third floor divides the strip on its own lines and is shown as it is.

3. Flat slab on the column grid, 300 mm structural zone, giving 3.00 m clear at every level and 3.30 m floor to floor; the penthouse is 3.25 m floor to top of slab.

4. The south cantilever is carried on all three upper floors and the penthouse. It projects 1.85 m at this cut, against 1.95 m at each end of the curve and 1.35 m at its waist, with a glass balustrade at the slab edge.

5. The penthouse stands clear of the north edge, leaving the roof terrace beyond its north wall. The corridor that joins the two terraces runs west of this cut and does not appear; see A-104.

6. The stair is drawn in thin line beyond the cut, where it is seen through the open spine. Foundations are indicative only and subject to a ground investigation and the engineer's design.

**FIVE-STOREY VACATION VILLA** — SHAMANDEEL, QUESNA, MENOUFIA, EGYPT

DRAWING

**SECTION A–A — DETACHED VILLA**

| DRAWING No | REVISION | SCALE | DATE |
|---|---|---|---|
| **A-200** | **P21** | **1:50 @ A1** | **2026-10-08** |

Final draft — layout agreed with the client; not for construction.
Do not scale; work to figured dimensions only.

REVISIONS

P18 2026-10-07 scheme A adopted: serpentine balcony on every plan; site named
P19 2026-10-07 serpentine waist deepened 0.75 to 1.35 m; 15.7 m² of balcony a floor
P20 2026-10-07 internal partitions 100 mm red brick, specified by the client
P21 2026-10-07 300 mm external and party walls: brick, colour unrestricted