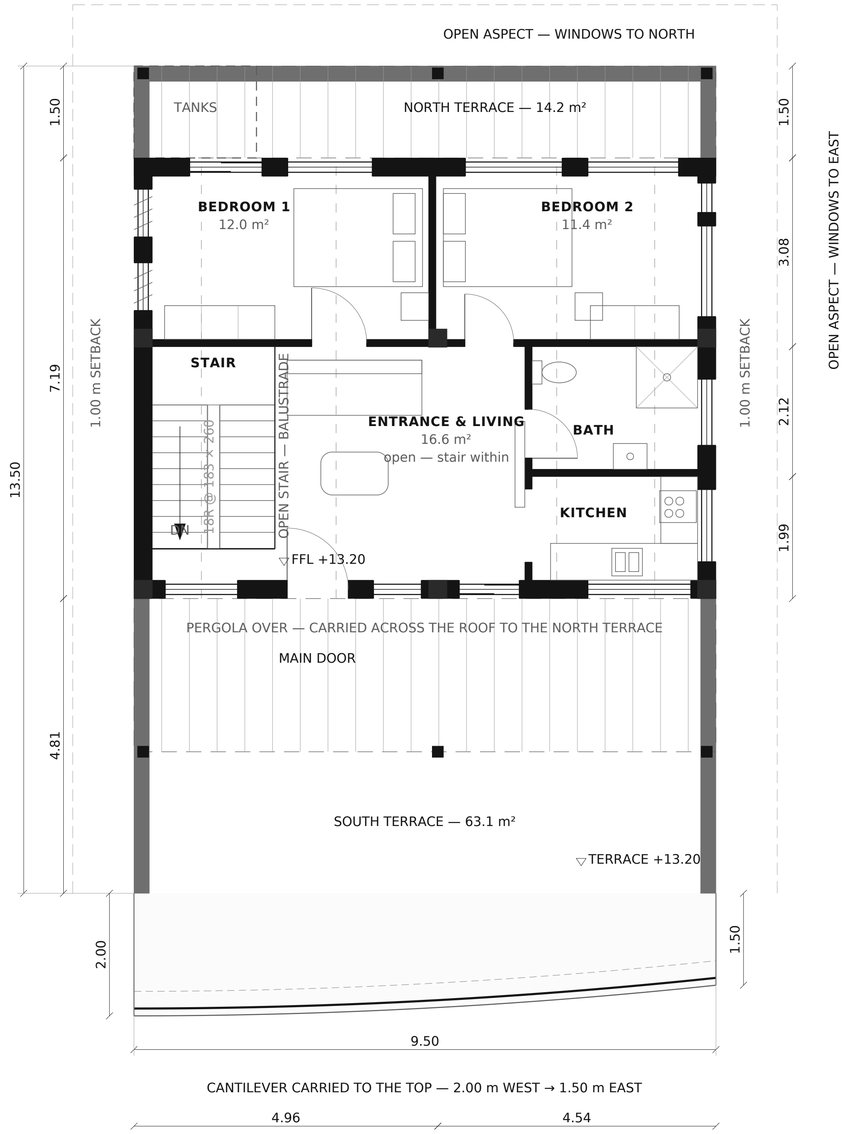

GRAPHIC SCALE 1:50

0 2 4 6 8 10 m

N

PENTHOUSE PLAN — DETACHED VILLA

LEVEL +13.20 · 1:50 @ A1 · METRES

KEY

- Masonry wall cut by section — 200 mm partition, 300 mm external / party
- Internal stud or block partition, 120 mm
- Terrace parapet, 250 mm × 1100 mm high
- Single leaf door, swing shown to opening side
- Glazed opening — arched head where noted
- Element above the cut plane (pergola, slab over)
- Void / open to sky
- ▽ +0.00 Finished floor level datum

AREA SCHEDULE

ENTRANCE AND LIVING	16.6 m²
STAIR	6.6 m²
KITCHEN	4.6 m²
BATH	5.4 m²
BEDROOM 1	12.0 m²
BEDROOM 2	11.4 m²
TOTAL	**56.6 m²**
GROSS INTERNAL AREA, PENTHOUSE	58.7 m²
ROOF TERRACE	63.1 m²
TOP OF PENTHOUSE SLAB	+16.45
FLOOR BELOW	+9.90

GENERAL NOTES

1. Draft for comment. A two-bedroom apartment between two terraces, with its own front door. 58.6 m² indoors, 63.1 m² of terrace to the south and 14.2 m² to the north.

2. The pergola is what joins them: a band on each terrace against the apartment, with its beams carried across the apartment's roof between. The terraces are open to the sky everywhere else.

3. The apartment runs wall to wall because it has to. Two bedrooms sit north of the stair side by side, and the only line to divide them on is the spine, which leaves 4.51 and 4.09 m. Take 1.50 m off the east for a covered walk and the second bedroom drops to 2.59 m wide, which is not a bedroom.

4. The stair ends at y 12.42 and cannot move, so the bedrooms' depth and the north terrace come out of the same 4.58 m. Flush north gives 18.5 m² bedrooms and no terrace at all; the north wall at 15.50 gives 12.0 and 11.4 m² and a 14.2 m² terrace. Both beds turn sideways in a 2.66 m deep room.

5. The south wall sits on the column grid at y 8.46, bearing on the beam between the columns at x 12.65, 17.46 and 21.85; the third floor under it is an open living area. East and west it sits on the walls below.

6. The site plan, section A—A and the A-300 enlargements are still on the old 11.50 × 14.50 footprint.

FOUR-STOREY VACATION HOME — PRIVATE CLIENT

DRAWING

PENTHOUSE PLAN — DETACHED VILLA

DRAWING No	REVISION	SCALE	DATE
A-104	**P10**	**1:50 @ A1**	**2026-10-06**

Preliminary design issue — not for construction.
Do not scale; work to figured dimensions only.

REVISIONS

P7 2026-10-06 second floor agreed; ground floor redrawn as the villa
P8 2026-10-06 ground floor opened up; guest room off the hall
P9 2026-10-06 penthouse added: two-bedroom roof apartment
P10 2026-10-06 penthouse between two terraces, pergola joining them