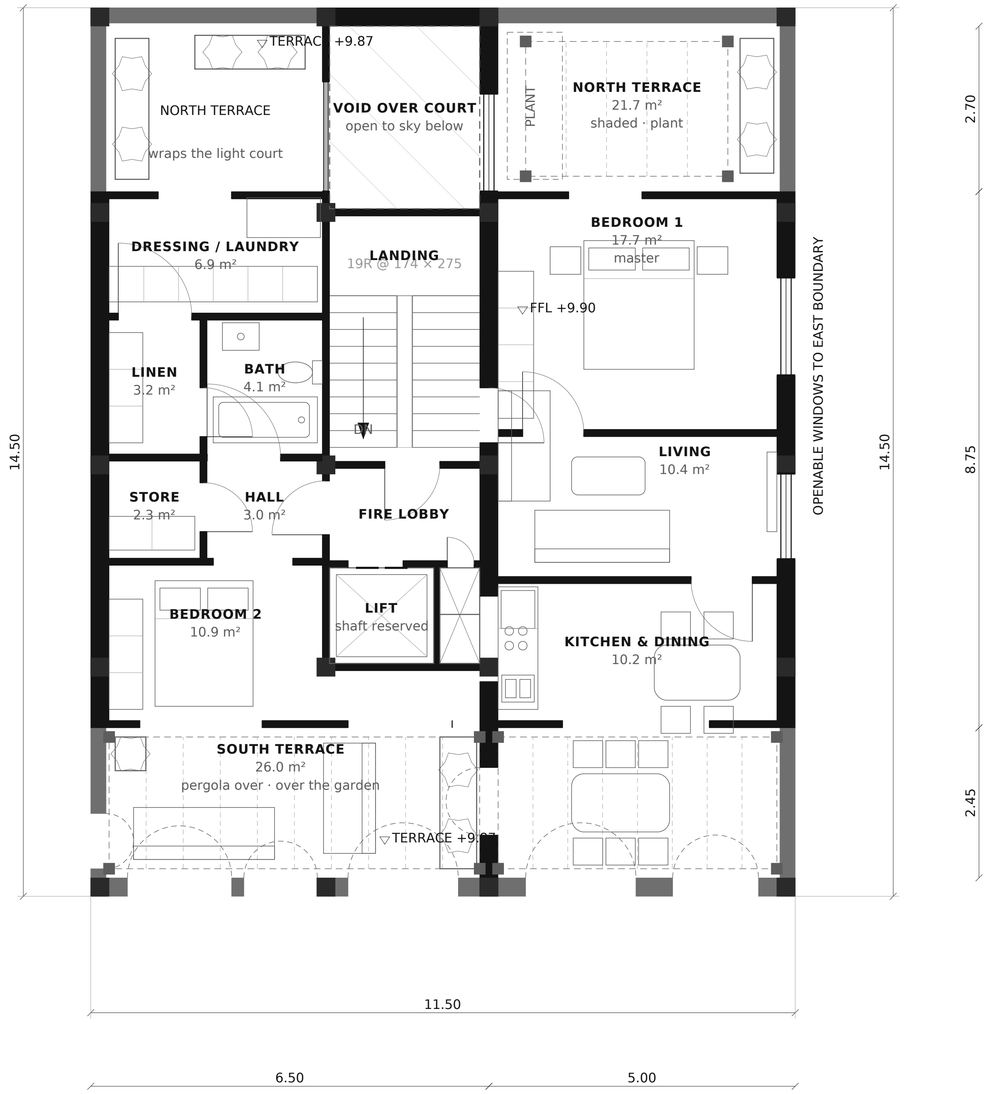

GRAPHIC SCALE 1:50

0 2 4 6 8 10 m

N

THIRD FLOOR & ROOF PLAN

LEVEL +9.90 · 1:50 @ A1 · METRES

KEY

- Masonry wall cut by section — 200 mm partition, 300 mm external / party
- Internal stud or block partition, 120 mm
- Terrace parapet, 250 mm × 1100 mm high
- Single leaf door, swing shown to opening side
- Glazed opening — arched head where noted
- Element above the cut plane (pergola, slab over)
- Void / open to sky
- ▽ +0.00 Finished floor level datum

AREA SCHEDULE

SOUTH TERRACE	26.0 m²
BEDROOM 2	10.9 m²
ENTRY HALL	3.0 m²
STORE	2.3 m²
FAMILY BATHROOM	4.1 m²
LINEN	3.2 m²
DRESSING & LAUNDRY	6.9 m²
LIFT SHAFT	2.7 m²
FIRE LOBBY	3.7 m²
PROTECTED STAIR	9.8 m²
KITCHEN & DINING	10.2 m²
LIVING	10.4 m²
BEDROOM 1	17.7 m²
NORTH TERRACE	21.7 m²
TOTAL	**132.5 m²**
GROSS INTERNAL AREA, THIS FLOOR	92.4 m²
OPEN-AIR TERRACE, NORTH AND SOUTH	47.7 m²
ROOF OVER, TOP OF SLAB	+13.20

GENERAL NOTES

1. A single two-bedroom apartment with a terrace on each side: the south terrace over the garden under a pergola, the north terrace shaded against the boundary wall and carrying the plant.

2. Living, kitchen and dining run through the party wall as one space and open onto the south terrace through 2.00 m and 2.40 m sliding screens.

3. Bedroom 1 takes block B with an openable east window above +3.00; bedroom 2 sits in block A and opens onto the south terrace. Bathroom, linen and store are internal, with mechanical extract to the riser.

4. Terrace finish is 30 mm below internal floor level, falling 1:80 to outlets at the parapet. Parapets are 250 mm thick and 1.10 m high above the terrace finish.

5. Condensers, the sprinkler tank and the roof plant stand on the north terrace behind a screen, clear of the usable area. The roof over falls 1:60 to outlets at the parapet, waterproofing turned up 150 mm minimum.

6. The light court is carried up through this floor and remains open to sky; the north terrace wraps it on both sides.

FOUR-STOREY VACATION HOME — PRIVATE CLIENT

DRAWING

THIRD FLOOR & ROOF PLAN

DRAWING No	REVISION	SCALE	DATE
A-103	**P3**	**1:50 @ A1**	**2026-09-29**

Preliminary design issue — not for construction.
Do not scale; work to figured dimensions only.

REVISIONS
P1 2026-09-18 first issue
P2 2026-09-24 east windows, taller floors, garden on A-100
P3 2026-09-29 four storeys, apartments, straight north boundary