GROUND FLOOR PLAN

LEVEL +0.00 · 1:50 @ A1 · METRES

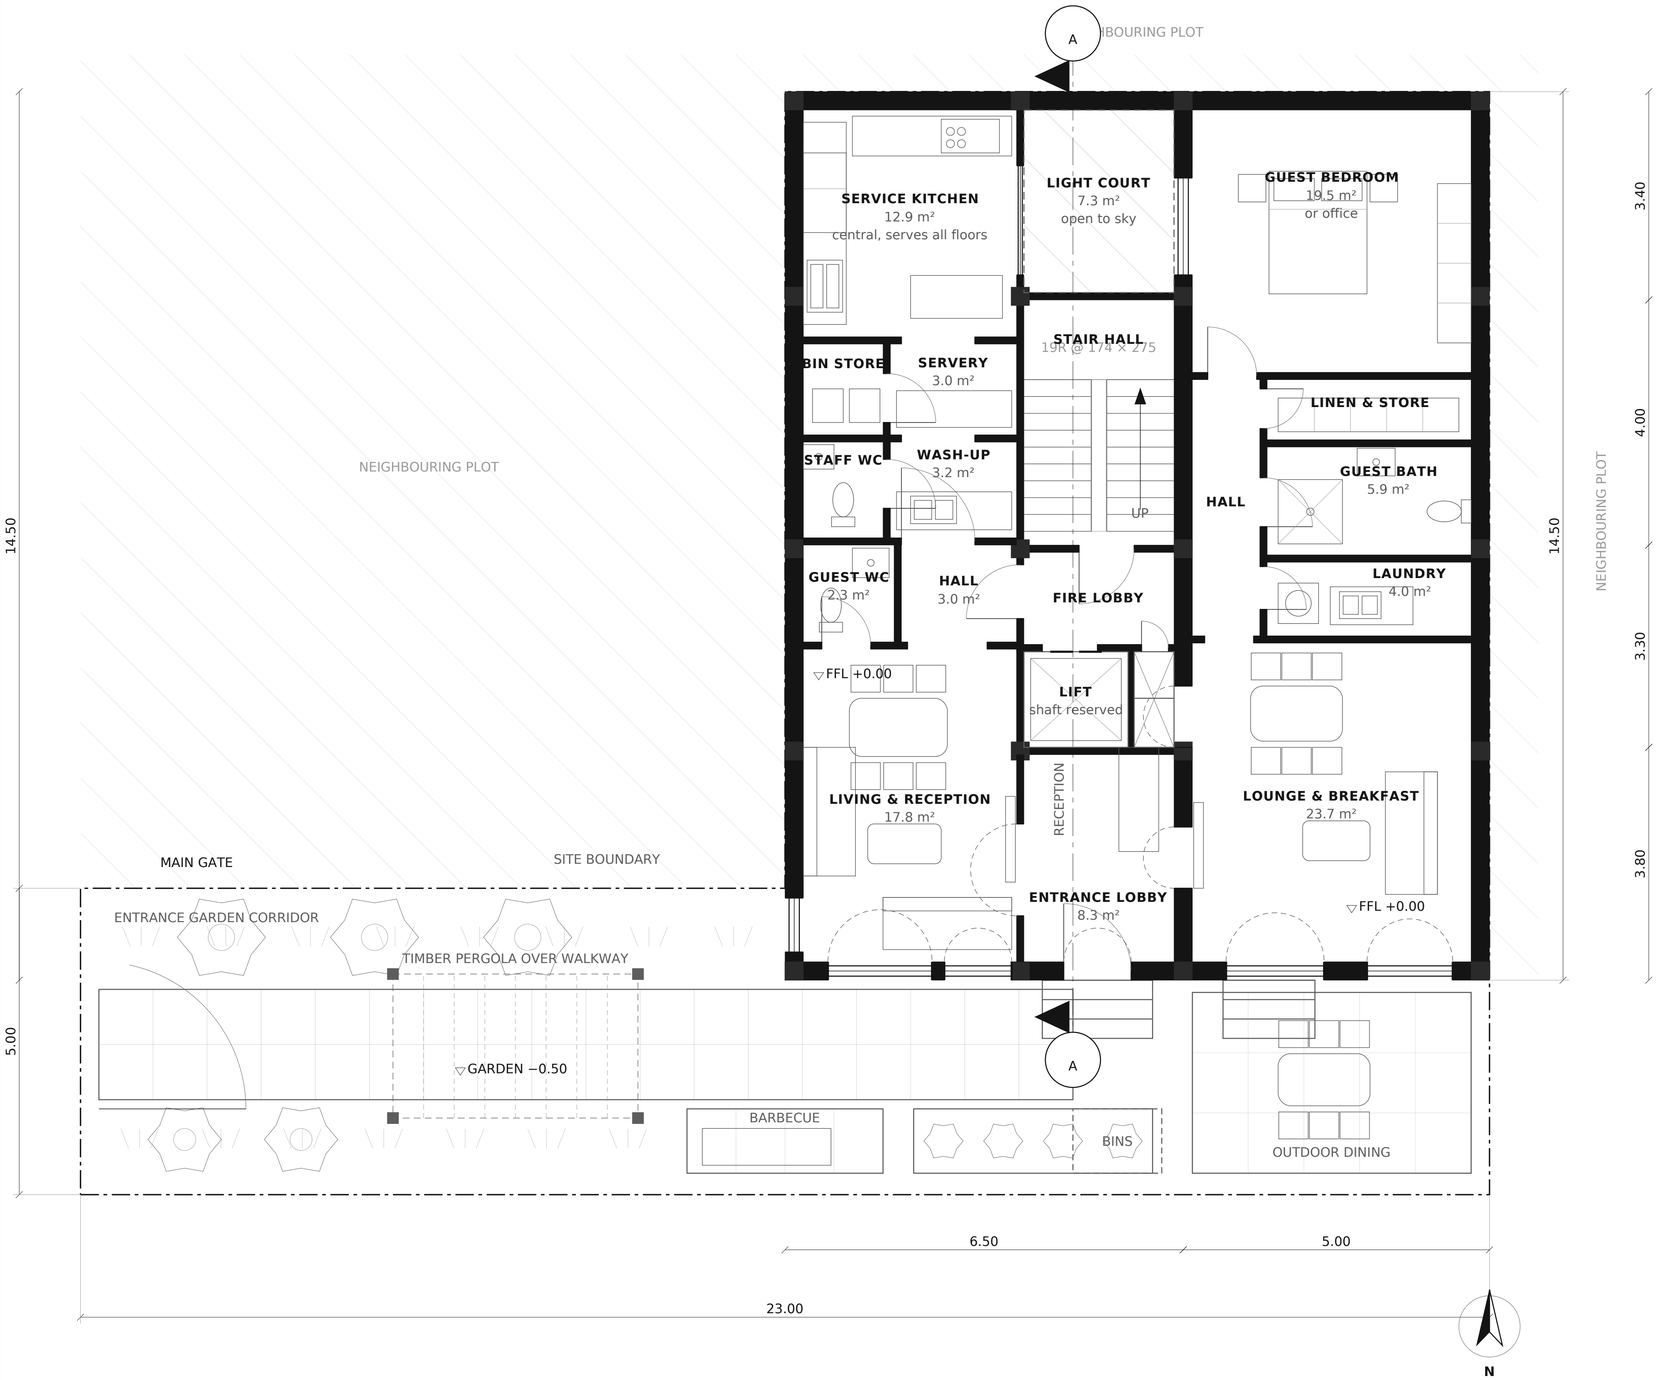

KEY

- Masonry wall cut by section — 200 mm partition, 300 mm external / party
- Internal stud or block partition, 120 mm
- Terrace parapet, 250 mm × 1100 mm high
- Single leaf door, swing shown to opening side
- Glazed opening — arched head where noted
- Element above the cut plane (pergola, slab over)
- Void / open to sky
- ▽ +0.00 — Finished floor level datum

AREA SCHEDULE

ENTRANCE LOBBY & RECEPTION	8.3 m²
LIVING & RECEPTION	17.8 m²
GUEST WC	2.3 m²
HALL	3.0 m²
STAFF WC	2.0 m²
WASH-UP	3.2 m²
BIN STORE	1.9 m²
SERVERY	3.0 m²
SERVICE KITCHEN	12.9 m²
LIFT SHAFT	2.7 m²
FIRE LOBBY	3.7 m²
PROTECTED STAIR	9.8 m²
LOUNGE & BREAKFAST	23.7 m²
HALL, BLOCK B	4.6 m²
CENTRAL LAUNDRY	4.0 m²
GUEST BATH	5.9 m²
LINEN & STORE	3.3 m²
GUEST BEDROOM	19.5 m²
TOTAL	**131.5 m²**
GROSS INTERNAL AREA, THIS FLOOR	140.0 m²
LIGHT COURT, OPEN TO SKY	7.3 m²
SLAB TO SLAB	3.30 m · 3.00 m clear

GENERAL NOTES

1. The whole of this floor is one non-residential compartment under the apartments: 2 hour separation to the floor over, sprinklered throughout, with a suppression hood over the cooking line.

2. The 12.9 m² service kitchen and the 4.0 m² laundry serve all four storeys, reached through the servery and the block B hall so that no room is entered through another. Kitchen extract rises in a fire-rated shaft in the riser cupboard off the fire lobby and discharges above roof level.

3. Living, reception, entrance lobby and the lounge read as one connected sequence through 1.00 m arched openings in the party wall. The guest WC opens off the reception and the guest bath off the block B hall, so neither is reached through the service route.

4. The east boundary wall is solid at this level: the adjoining owner may build up to 3.00 m against it. The kitchen and the guest bedroom are daylit from the light court, and the west wall is opened where it faces our own garden boundary — 3.00.

5. Bins are stored internally beside the kitchen. Guest bath, laundry, WCs and stores are internal, mechanically extracted at six air changes per hour. Gross internal area excludes the light court.

FOUR STOREY VACATION HOME — PRIVATE CLIENT

DRAWING

GROUND FLOOR PLAN

DRAWING No	REVISION	SCALE	DATE
A-100	**P3**	**1:50 @ A1**	**2026-09-29**

Preliminary design issue — not for construction.
Do not scale; work to figured dimensions only.

REVISIONS

P1 2026-09-18 first issue
P2 2026-09-24 east windows, taller floors, garden on A-100
P3 2026-09-29 four storeys, apartments, straight north boundary