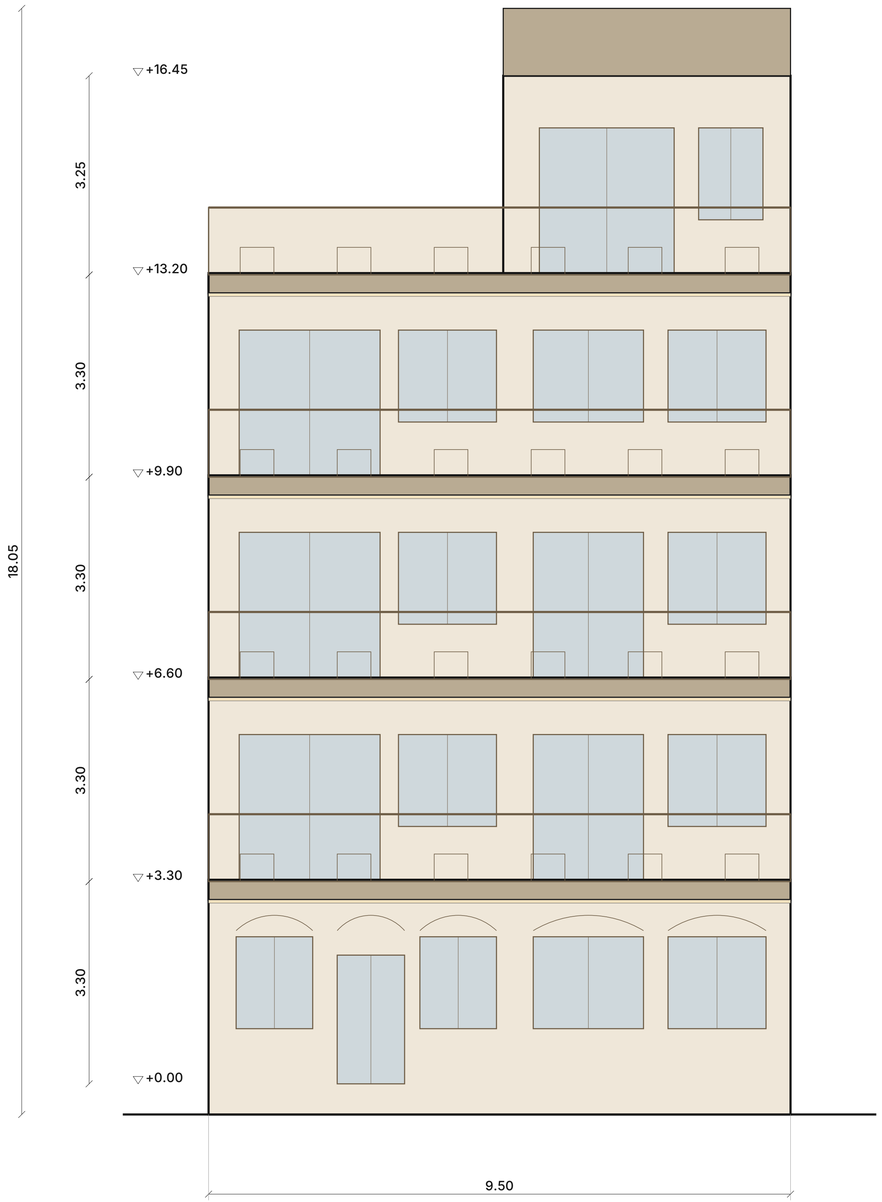

THE BALCONY CURVE IN PLAN — IT CANNOT SHOW IN ELEVATION

1.95 m DEEPEST · 0.90 m SHALLOWEST · 14.9 m² A FLOOR

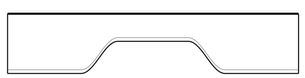

GRAPHIC SCALE 1:100

0 2 4 m

SOUTH ELEVATION — SCHEME C “FACET”

LEVEL street frontage · 1:50 @ A1 · METRES

KEY

- External / party wall cut by section, 300 mm — brick, colour unrestricted
- Internal partition, 100 mm — red brick
- Terrace parapet, 250 mm × 1100 mm high
- Single leaf door, swing shown to opening side
- Glazed opening — arched head where noted
- Element above the cut plane (pergola, slab over)
- Void / open to sky
- ▽ +0.00 Finished floor level datum

SCHEME C — FACET

WALLS	warm limestone render
SLAB NOSING	rounded, 180 mm
COVE LIGHT	in the underside of the nosing
BALUSTRADE	clear glass, 120 mm inboard
FRAMES	bronze anodised
BALCONY CURVE	straight runs, radiused
PROJECTION	1.95 / 0.90 m
STRAIGHT FORMWORK	7.10 of 9.50 m
BALCONY AREA	14.9 m² a floor
TOP OF BUILDING	+17.55

GENERAL NOTES

1. The exterior only. The plans, site plan and section are agreed and re-issued to the adopted curve; nothing here changes the rest of them: same five levels, same 9.50 × 13.50 m footprint, same 1.00 m setbacks, same openings. Only the skin differs between the schemes.

2. Every opening drawn here is read from the plan it belongs to rather than redrawn, and checks.py fails the build if an elevation ever shows one the plan does not have.

3. Scheme C is scheme A's skin exactly — warm limestone, cove-lit slab nosings, glass balustrades, planting, the same arched ground floor. Only the balcony curve differs, which is the whole point of putting it beside A.

4. The curve is the serpentine built out of straight runs: 2.40 m flat at 1.95 m deep at each end, a flat waist at 0.90 m in the middle, and 1.20 m radiused transitions between. Every joint is a tangent, so from the street the eye still reads one continuous edge.

5. What recommends it is the formwork: straight for 7.10 m of the 9.50 m span rather than curved end to end. It also carried more area than the serpentine as first drawn; raising that curve's waist to 1.35 m reversed it, and scheme A now carries 15.7 m² a floor against this one's 14.9.

6. It is not the adopted curve. Scheme A was chosen and the plans are drawn to its serpentine; moving to this one now would re-issue A-000 and A-100 to A-104 a second time, and give up 3 m² of balcony.

7. The balconies do not wrap the corner: the 1.00 m setbacks forbid anything projecting west, north or east, so the cantilever stays on the street frontage.

FIVE-STOREY VACATION VILLA — EZBIT ABU RUKBAH, QUESNA, MENOUFIA, EGYPT

DRAWING

SOUTH ELEVATION — SCHEME C “FACET”

DRAWING No	REVISION	SCALE	DATE
A-420	**P32**	**1:50 @ A1**	**2026-10-13**

Option not selected — scheme A “Wave” was adopted at P18. Record only; not for construction.
Do not scale; work to figured dimensions only.

REVISIONS

P29 2026-10-11 STR-200: the column schedule it was named for; heights corrected
P30 2026-10-12 site corrected to Ezbit Abu Rukbah; Code 305 named as the fire code
P31 2026-10-12 ground parameters recorded on GEO-002; water table given as 2.50 m
P32 2026-10-13 roof access: ladder to +16.45, guard at 1.10, top now +17.55