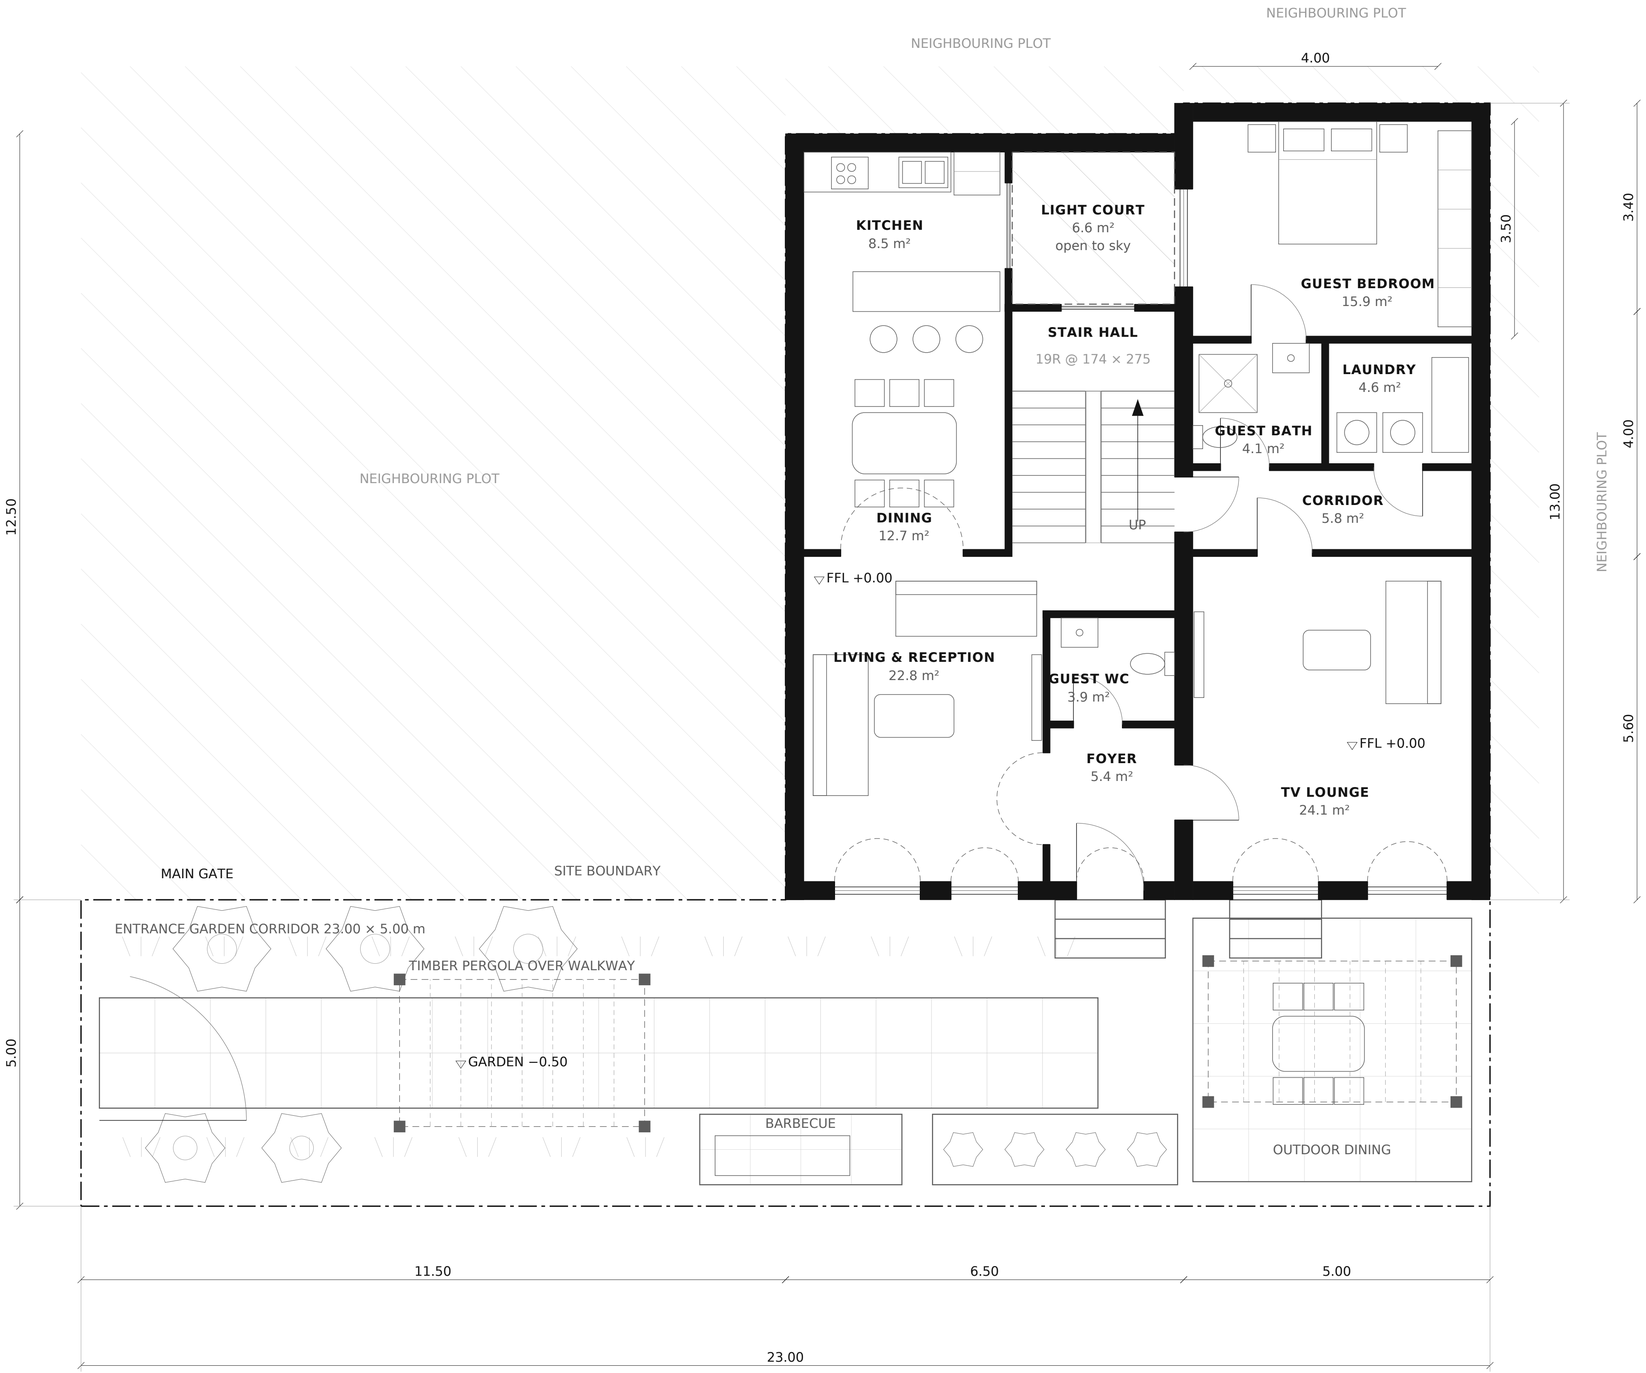

GROUND FLOOR PLAN

LEVEL +0.00 · 1:50 @ A1 · METRES

KEY

- Masonry wall cut by section — 200 mm partition, 300 mm external / party
- Internal stud or block partition, 120 mm
- Terrace parapet, 250 mm × 1100 mm high
- Single leaf door, swing shown to opening side
- Glazed opening — arched head where noted
- Element above the cut plane (pergola, slab over)
- Void / open to sky
- ▽ +0.00 — Finished floor level datum

AREA SCHEDULE

LIVING & RECEPTION	22.8 m²
ENTRANCE FOYER	5.4 m²
GUEST WC	3.9 m²
DINING	12.7 m²
KITCHEN	8.5 m²
STAIR HALL	10.6 m²
LIGHT COURT	6.6 m²
TV LOUNGE	24.1 m²
CORRIDOR	5.8 m²
GUEST BATH	4.1 m²
LAUNDRY & STORE	4.6 m²
GUEST BEDROOM	15.9 m²
TOTAL	**125.0 m²**
GROSS INTERNAL AREA, THIS FLOOR	121.8 m²
SLAB TO SLAB	3.30 m · 3.00 m clear

GENERAL NOTES

1. Living, dining and kitchen read as one space, linked by 2.00 m and 1.50 m wide arched openings; arch heads are shown dashed.
2. South elevation glazing to the living room and TV lounge is arched and faces the 23 m garden corridor.
3. The ground floor sits 0.50 m above the garden: three risers at 167 mm at the entrance and at the patio doors. Garden level −0.50, finished floor level +0.00.
4. The east boundary wall is solid at this level: the adjoining owner may build up to 3.00 m against it. Every room here is ventilated from the garden elevation or the light court.
5. Guest bath and laundry are internal rooms: mechanical extract to the light court at six air changes per hour.
6. The guest bedroom is single sided onto the light court, and is 4.00 × 3.50 m clear of the fitted wardrobe. Its door is undercut 15 mm to draw make-up air from the corridor.
7. Gross internal area excludes the light court.

VACATION HOUSE — NEW BUILD — PRIVATE CLIENT

DRAWING

GROUND FLOOR PLAN

DRAWING No	REVISION	SCALE	DATE
A-100	**P1**	**1:50 @ A1**	**2026-09-18**

Preliminary design issue — not for construction.
Do not scale; work to figured dimensions only.