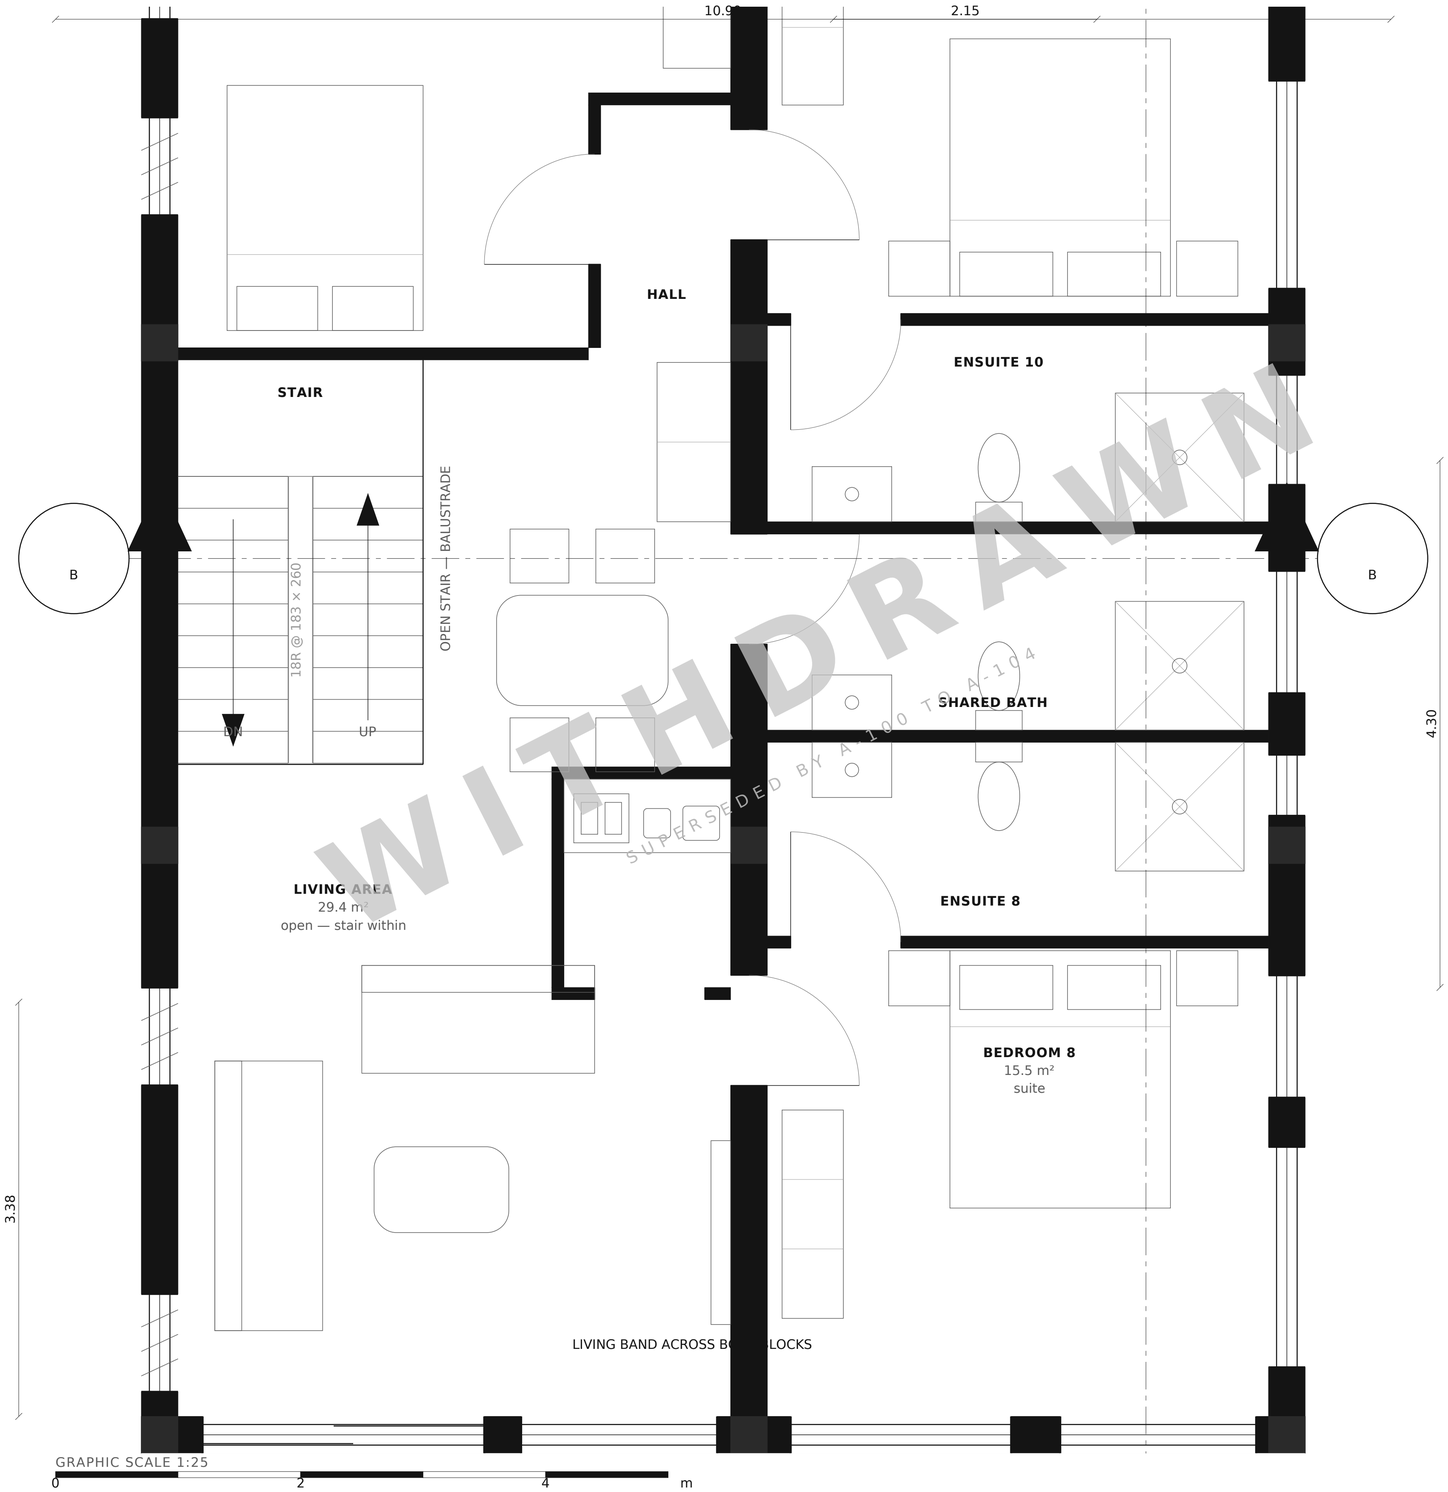

WITHDRAWN
SUPERSEDED BY A-100 TO A-104

THIRD FLOOR APARTMENT — ENLARGED PLAN

LEVEL +9.90 · 1:25 @ A1 · METRES

KEY

- External / party wall cut by section, 300 mm — brick, colour unrestricted
- Internal partition, 100 mm — red brick
- Terrace parapet, 250 mm × 1100 mm high
- Single leaf door, swing shown to opening side
- Glazed opening — arched head where noted
- Element above the cut plane (pergola, slab over)
- Void / open to sky
- ▽ +0.00 — Finished floor level datum

AREA SCHEDULE

LIVING / DINING / KITCHEN	35.8 m²
BEDROOM 1	19.6 m²
ENSUITE	7.5 m²
DRESSING	7.1 m²
FAMILY BATH	5.2 m²
GUEST WC	2.3 m²
TOTAL	**77.5 m²**
APARTMENT, GROSS INTERNAL	≈116 m²
SOUTH TERRACE / NORTH TERRACE	13.8 / 12.3 m²

GENERAL NOTES

1. Enlarged from A-103. The party wall can only be opened between y 3.80 and 7.18, so the living, dining and kitchen occupy that whole band as one 10.60 m wide room and form the only link between the two blocks.

2. Bedroom 1 and its ensuite take block B, windowed on the open east boundary. The ensuite is entered from the dressing room, and the dressing room from bedroom 1.

3. Block A carries the entry hall on the front door, with the guest WC, the store, the family bath and its passage off it, and bedroom 2 beyond — 18.0 m² across the whole north end, with two windows in the north wall.

4. No room on this floor is entered through another.

FIVE-STOREY VACATION VILLA — SHAMANDEEL, QUESNA, MENOUFIA, EGYPT

DRAWING

THIRD FLOOR APARTMENT — ENLARGED PLAN

DRAWING No	REVISION	SCALE	DATE
A-301	**P22**	**1:25 @ A1**	**2026-10-12**

Withdrawn at P22 — superseded by A-100 to A-104. Record only; not for construction, pricing or measurement. Do not scale; work to figured dimensions only.

REVISIONS

P19 2026-10-07 serpentine waist deepened 0.75 to 1.35 m; 15.7 m² of balcony a floor
P20 2026-10-07 internal partitions 100 mm red brick, specified by the client
P21 2026-10-07 300 mm external and party walls: brick, colour unrestricted
P22 2026-10-08 A-300 to A-302 withdrawn: enlargements of a building not being built