# EXTERNAL WORKS & LANDSCAPE

LEVEL -0.50 garden, +0.00 villa · 1:75 @ A1 · METRES

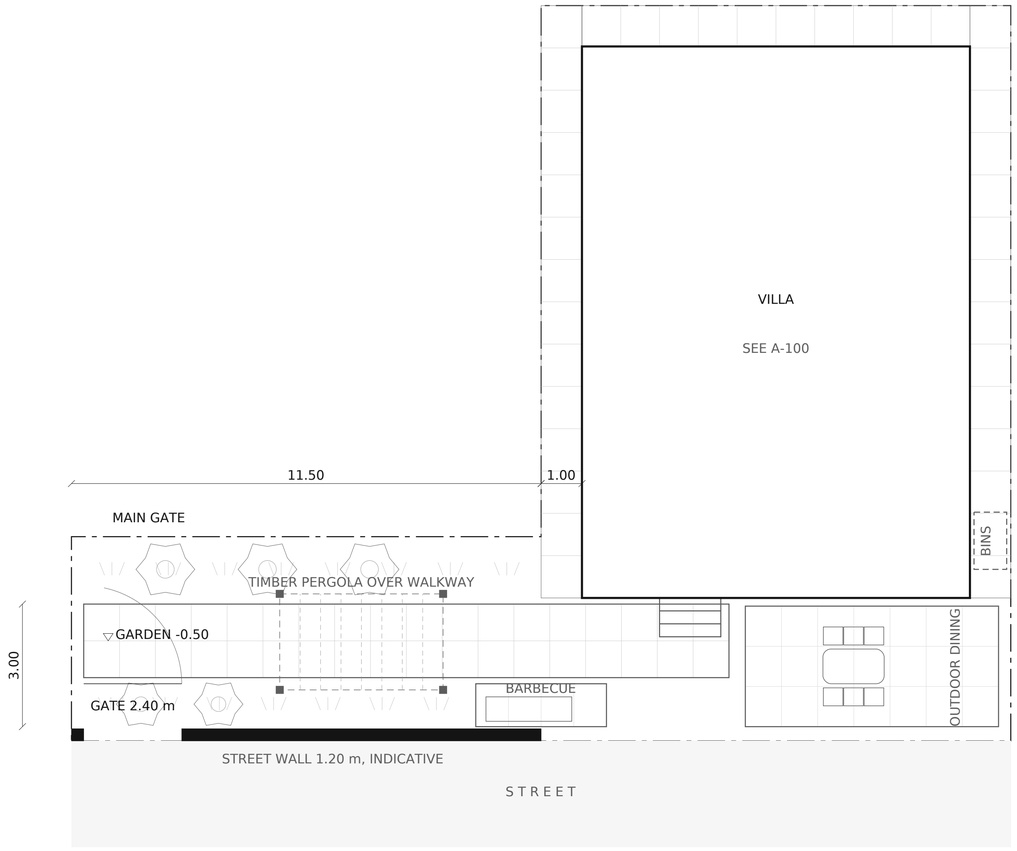


GRAPHIC SCALE 1:75

0 2 4 6 8 10 m

N

## KEY

- External / party wall cut by section, 300 mm — brick, colour unrestricted
- Internal partition, 100 mm — red brick
- Terrace parapet, 250 mm × 1100 mm high
- Single leaf door, swing shown to opening side
- Glazed opening — arched head where noted
- Element above the cut plane (pergola, slab over)
- Void / open to sky
- ▽ +0.00 — Finished floor level datum

## AREA SCHEDULE

| | |
|---|---|
| PAVED WALK | 28.4 m² |
| FORECOURT | 18.3 m² |
| BARBECUE TERRACE | 3.4 m² |
| SIDE PASSAGES | 38.5 m² |
| TURF | 24.7 m² |
| **TOTAL** | **113.3 m²** |
| PERGOLA OVER THE WALK | 9.4 m² timber |
| TREES | 5 nr |
| STREET WALL | 9.10 m at 1.20 m, indicative |
| GATE | 2.40 m leaf |
| STEPS TO THE FRONT DOOR | 3 risers |
| PLOT LESS THE VILLA | 136.2 m² |
| NOT MEASURED HERE | 23.0 m² |

## GENERAL NOTES

1. The garden as a trade package rather than as context. Every area is read from the constants A-000 draws from, so this sheet and the site plan cannot disagree about a width.

2. The three 1.00 m setbacks are our own land and are paved as side passages, reached from the forecourt on the east and the garden on the west. They are the largest paved item on the sheet.

3. The street wall is 1.20 m high and INDICATIVE: its height, its coping and its finish await the client, and its line awaits the measured survey. Nothing else on the sheet depends on it.

4. Paving materials, bedding, falls, sub-base, turf specification and irrigation are not set by the geometry and are not invented here. The quantities are ours; the specification is not.

5. The forecourt is overhung by the balcony for up to 1.95 m, which is what covers the front door without a porch. See A-000 and A-400.

6. The schedule measures ground cover, so the pergola is listed beside it rather than in it - it stands over paving already counted. 23.0 m² of the plot outside the villa is not measured here: margins, the bin standing and the entrance steps. It is shown rather than absorbed.

**FIVE-STOREY VACATION VILLA** — SHAMANDEEL, QUESNA, MENOUFIA, EGYPT

DRAWING

**EXTERNAL WORKS & LANDSCAPE**

| DRAWING No | REVISION | SCALE | DATE |
|---|---|---|---|
| **ARC-700** | **P21** | **1:75 @ A1** | **2026-10-11** |

Preliminary design issue — not for construction.
Do not scale; work to figured dimensions only.

REVISIONS

P18 2026-10-07 scheme A adopted: serpentine balcony on every plan; site named
P19 2026-10-07 serpentine waist deepened 0.75 to 1.35 m; 15.7 m² of balcony a floor
P20 2026-10-07 internal partitions 100 mm red brick, specified by the client
P21 2026-10-07 300 mm external and party walls: brick, colour unrestricted